THESE DRAWINGS ARE FREE FOR YOU TO SHARE, MODIFY, AND DUPLICATE. THIS WORK DOESN'T REPRESENT A LEGAL CONTRACT OR CONSTITUTE ARCHITECTURAL SERVICES. NO PERSON OR ORGANIZATION MAKES ANY WARRANTY REGARDING THE INFORMATION PROVIDED. THE CREATORS DISCLAIM LIABILITY FOR ANY DAMAGES RESULTING FROM ITS USE. THIS WORK IS AVAILABLE UNDER A CREATIVE COMMONS ATTRIBUTION SHARE-ALIKE LICENSE. SOME RIGHTS RESERVED.

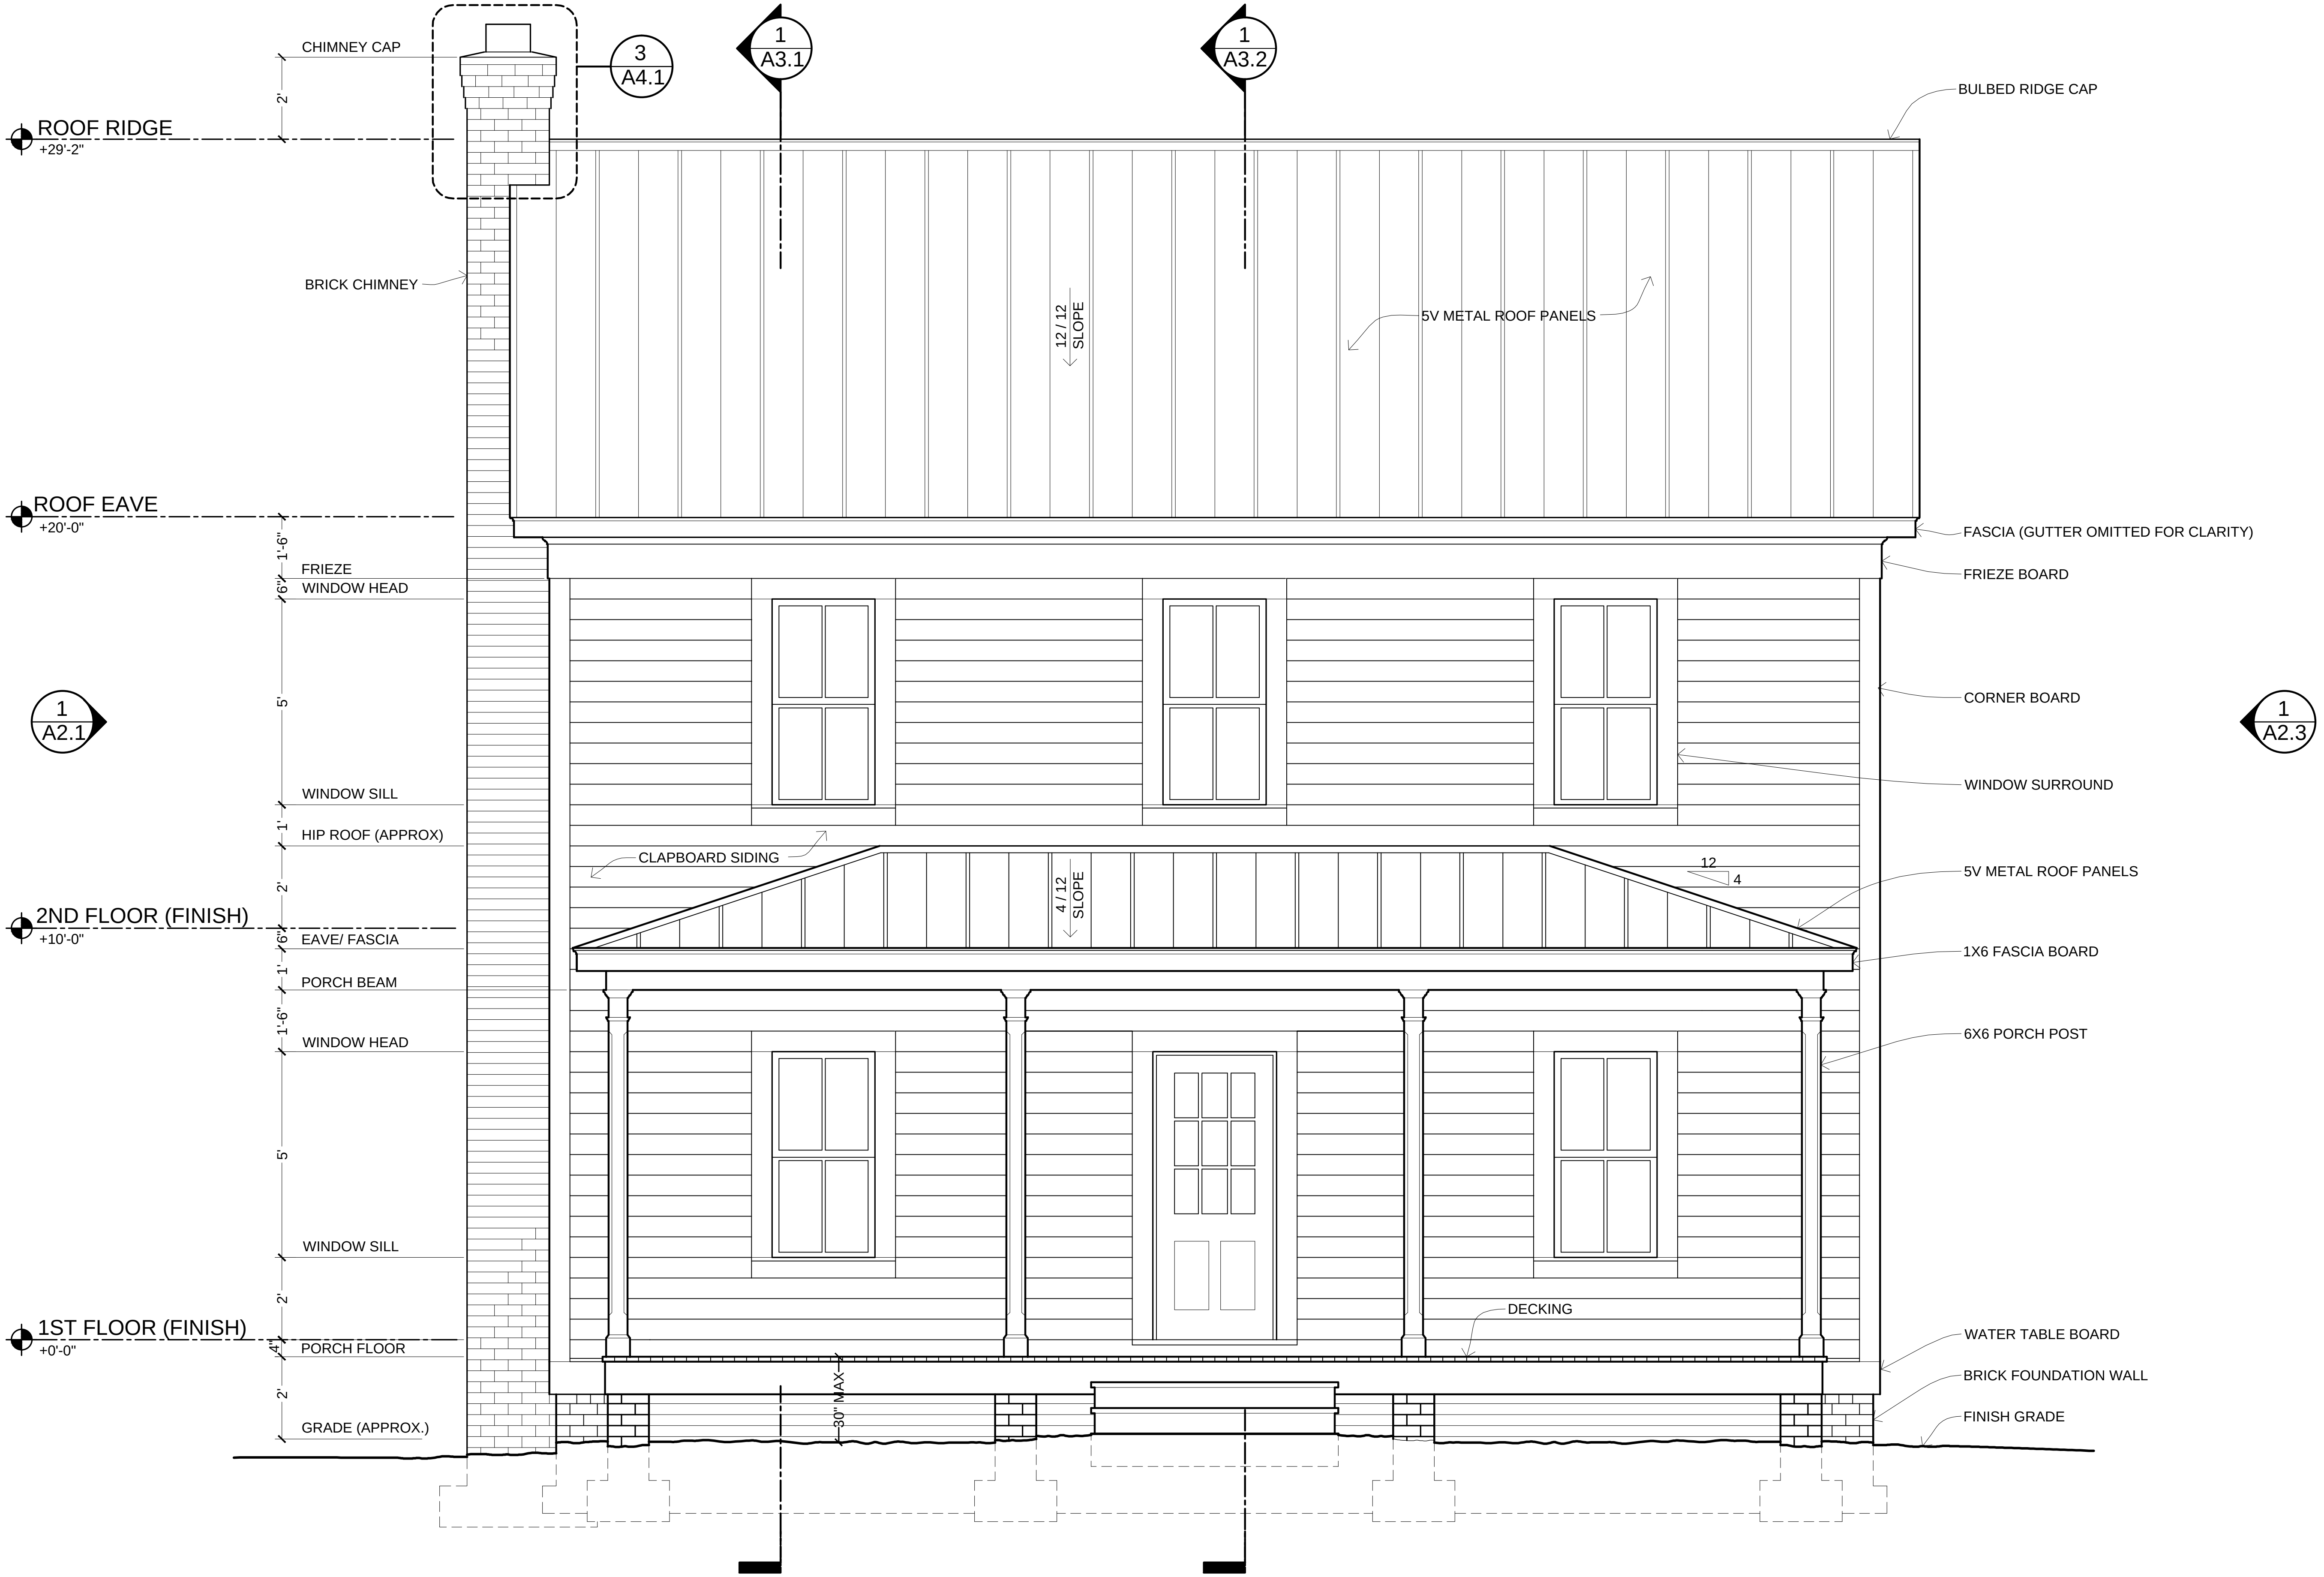
CHIMNEY CAP
3
A4.1
1
A3.1
1
A3.2
BULBED RIDGE CAP
ROOF RIDGE
+29'-2"
2'
BRICK CHIMNEY
12 / 12
SLOPE
5V METAL ROOF PANELS
ROOF EAVE
+20'-0"
FASCIA (GUTTER OMITTED FOR CLARITY)
1'-6"
FRIEZE
FRIEZE BOARD
6"
WINDOW HEAD
5'
CORNER BOARD
1
A2.1
1
A2.3
WINDOW SURROUND
WINDOW SILL
1'
HIP ROOF (APPROX)
CLAPBOARD SIDING
12
4
5V METAL ROOF PANELS
4 / 12
SLOPE
2'
2ND FLOOR (FINISH)
+10'-0"
6"
EAVE/ FASCIA
1X6 FASCIA BOARD
1'
PORCH BEAM
1'-6"
WINDOW HEAD
6X6 PORCH POST
5'
WINDOW SILL
2'
DECKING
1ST FLOOR (FINISH)
+0'-0"
WATER TABLE BOARD
4"
PORCH FLOOR
BRICK FOUNDATION WALL
2'
30" MAX
FINISH GRADE
GRADE (APPROX.)

① FRONT ELEVATION (SOUTH)

SCALE: 1/4" =1'-0"

OPEN-SOURCE BLUEPRINTS

CAD FILES AVAILABLE:
www.amatect.com/farmhouse
www.commons.wikimedia.org
/wiki/File:FarmhouseV-001.svg
openarchitecturenetwork.org
/projects/farmhouse

ORIGINAL DESIGNER
Jay Osborne, 2014

VIRGINIA'S FARMHOUSE

123 YELLOW BRICK RD, YOURTOWN, US

REVISION

△	VERSION 0.01 02-15-2015
△	
△	
△	
△	

DATE

02-15-15

SHEET TITLE

SOUTH ELEVATION

SHEET NO.

A2.0

THESE DRAWINGS ARE FREE FOR YOU TO SHARE, MODIFY, AND DUPLICATE. THIS WORK DOESN'T REPRESENT A LEGAL CONTRACT OR CONSTITUTE ARCHITECTURAL SERVICES. NO PERSON OR ORGANIZATION MAKES ANY WARRANTY REGARDING THE INFORMATION PROVIDED. THE CREATORS DISCLAIM LIABILITY FOR ANY DAMAGES RESULTING FROM ITS USE. THIS WORK IS AVAILABLE UNDER A CREATIVE COMMONS ATTRIBUTION SHARE-ALIKE LICENSE. SOME RIGHTS RESERVED.

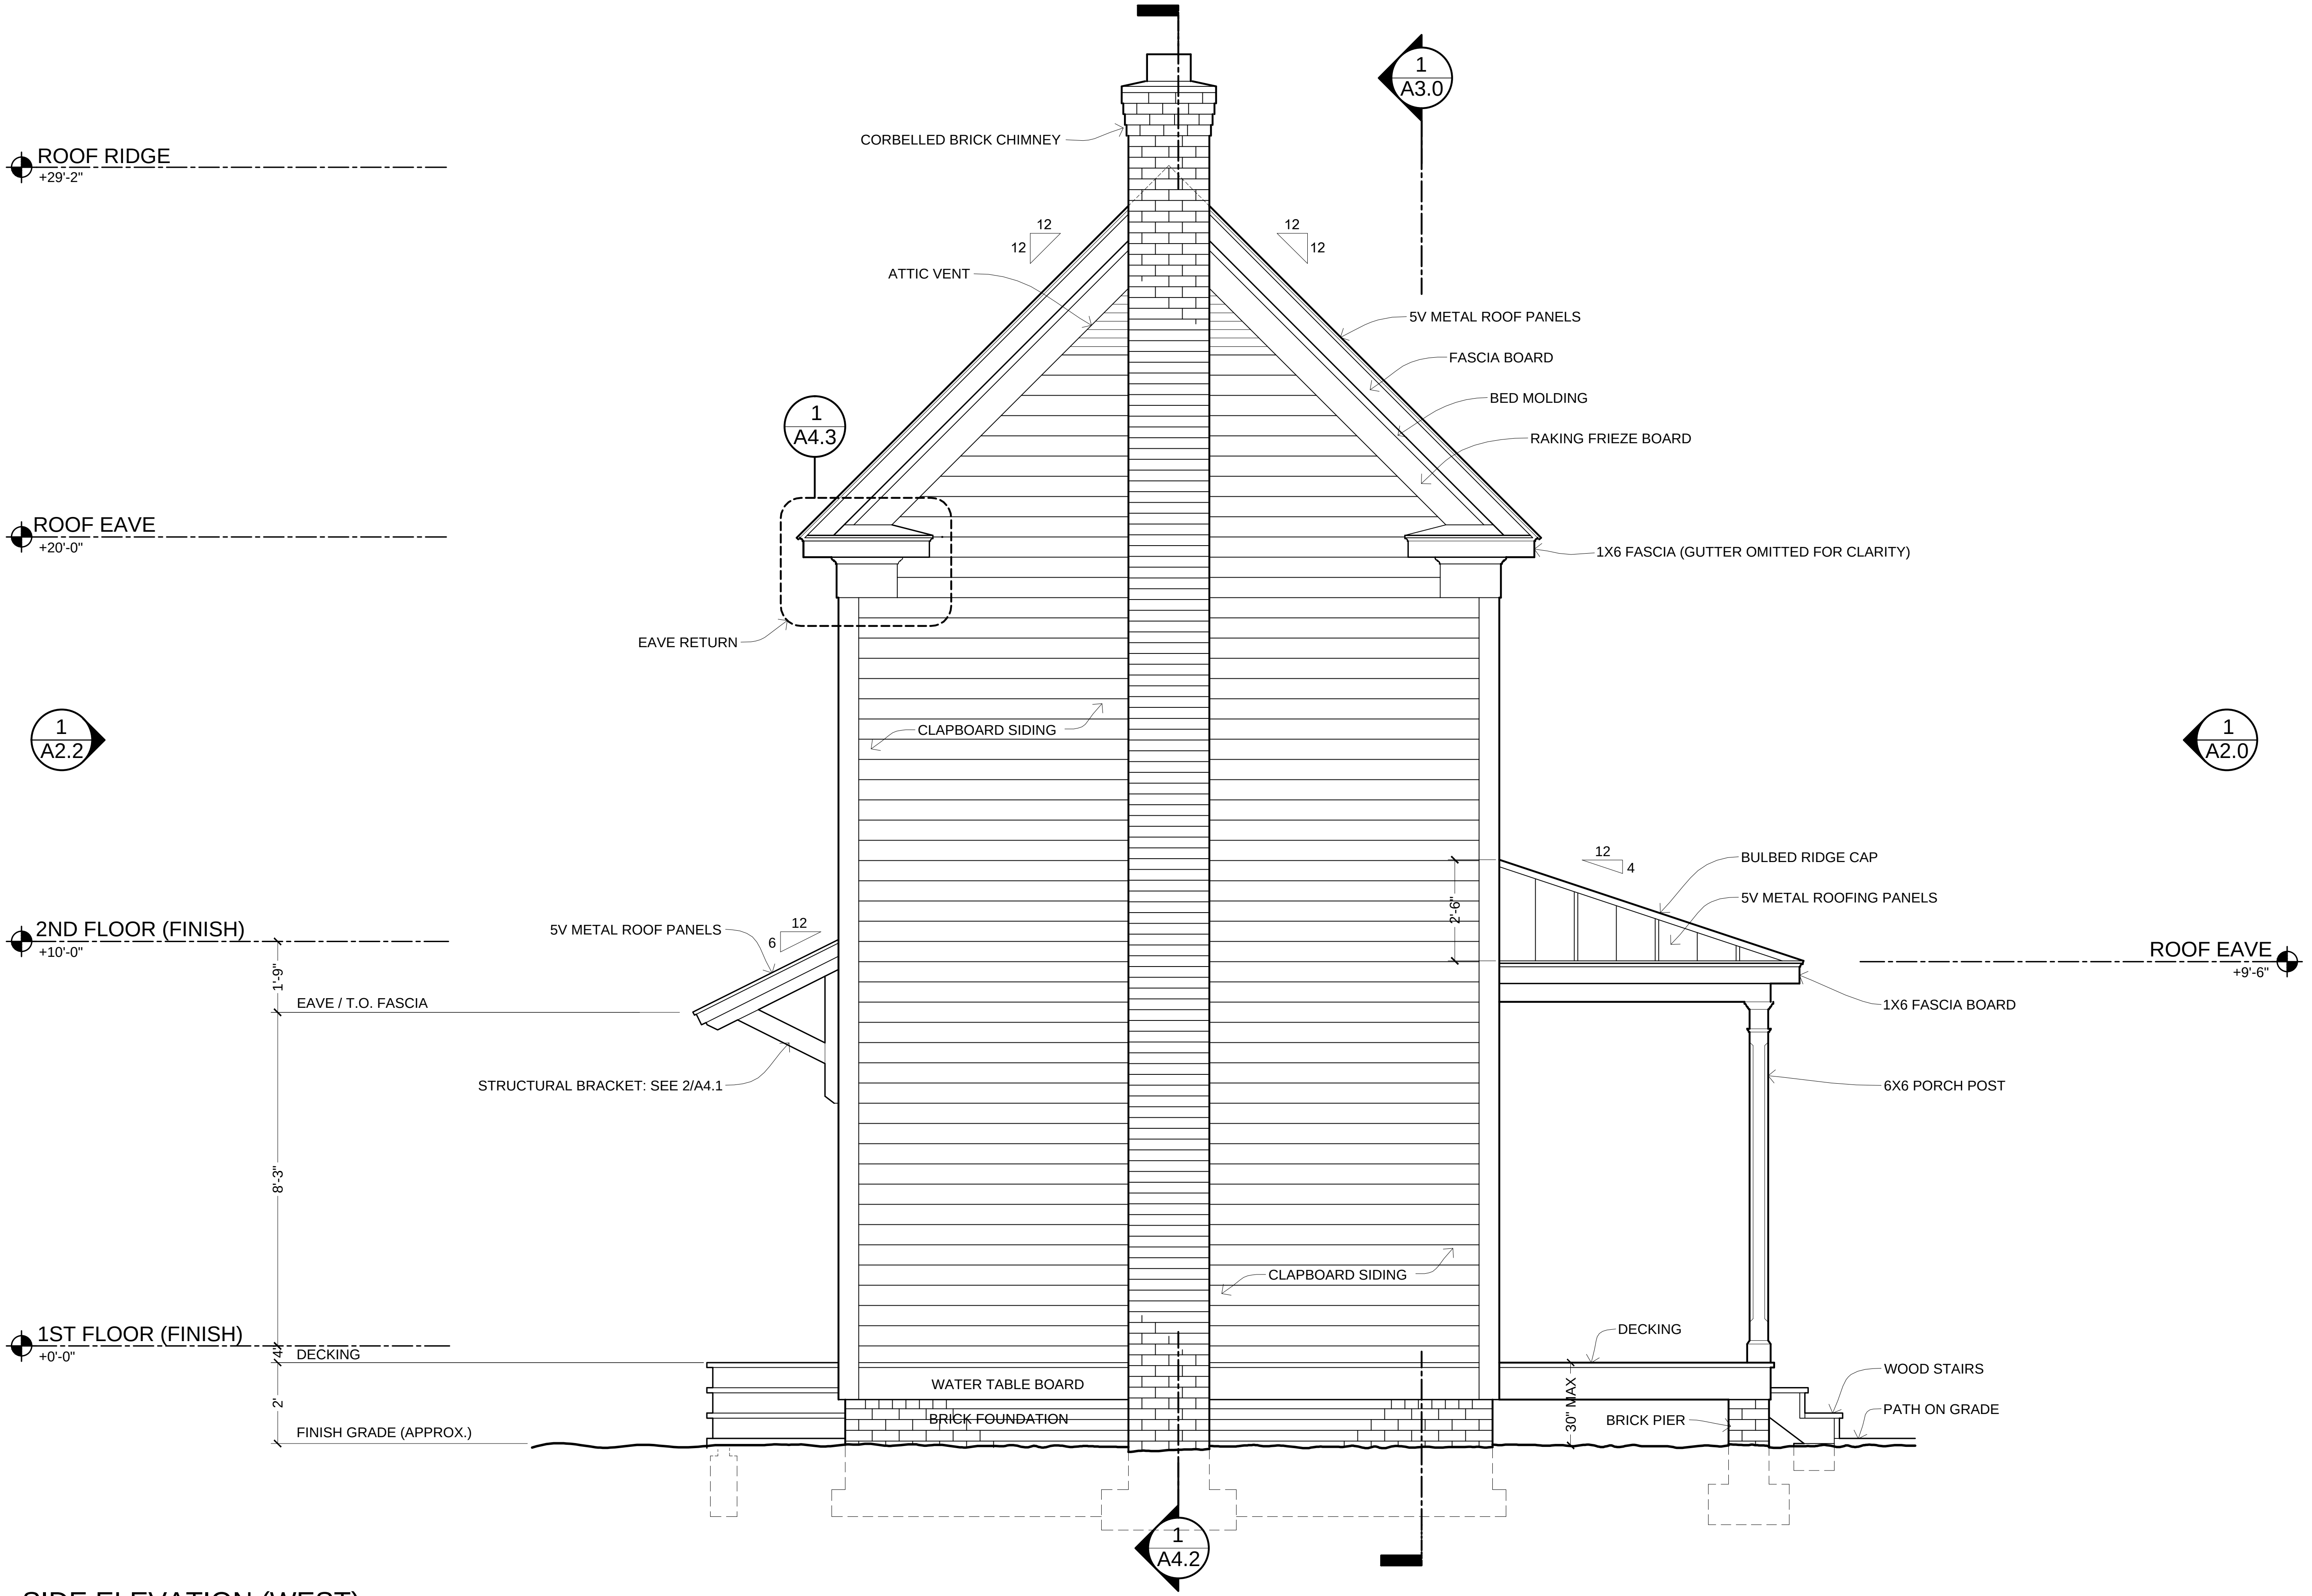
ROOF RIDGE
+29'-2"
ROOF EAVE
+20'-0"
2ND FLOOR (FINISH)
+10'-0"
1ST FLOOR (FINISH)
+0'-0"
1'-9"
EAVE / T.O. FASCIA
8'-3"
4"
DECKING
2'
FINISH GRADE (APPROX.)
1
A2.2
1
A4.3
EAVE RETURN
CORBELLED BRICK CHIMNEY
ATTIC VENT
12
12
12
12
1
A3.0
5V METAL ROOF PANELS
FASCIA BOARD
BED MOLDING
RAKING FRIEZE BOARD
1X6 FASCIA (GUTTER OMITTED FOR CLARITY)
CLAPBOARD SIDING
1
A2.0
12
4
BULBED RIDGE CAP
5V METAL ROOFING PANELS
2'-6"
ROOF EAVE
+9'-6"
1X6 FASCIA BOARD
5V METAL ROOF PANELS
12
6
STRUCTURAL BRACKET: SEE 2/A4.1
6X6 PORCH POST
CLAPBOARD SIDING
DECKING
WOOD STAIRS
WATER TABLE BOARD
30" MAX
PATH ON GRADE
BRICK FOUNDATION
BRICK PIER
1
A4.2

① SIDE ELEVATION (WEST)

SCALE: 1/4" =1'-0"

OPEN-SOURCE BLUEPRINTS

CAD FILES AVAILABLE:
www.amatect.com/farmhouse
www.commons.wikimedia.org
/wiki/File:FarmhouseV-001.svg
openarchitecturenetwork.org
/projects/farmhouse

ORIGINAL DESIGNER
Jay Osborne, 2014

VIRGINIA'S FARMHOUSE

123 YELLOW BRICK RD, YOURTOWN, US

REVISION

△	VERSION 0.01 02-15-2015
△	
△	
△	
△	

DATE

02-15-15

SHEET TITLE

WEST ELEVATION

SHEET NO.

A2.1

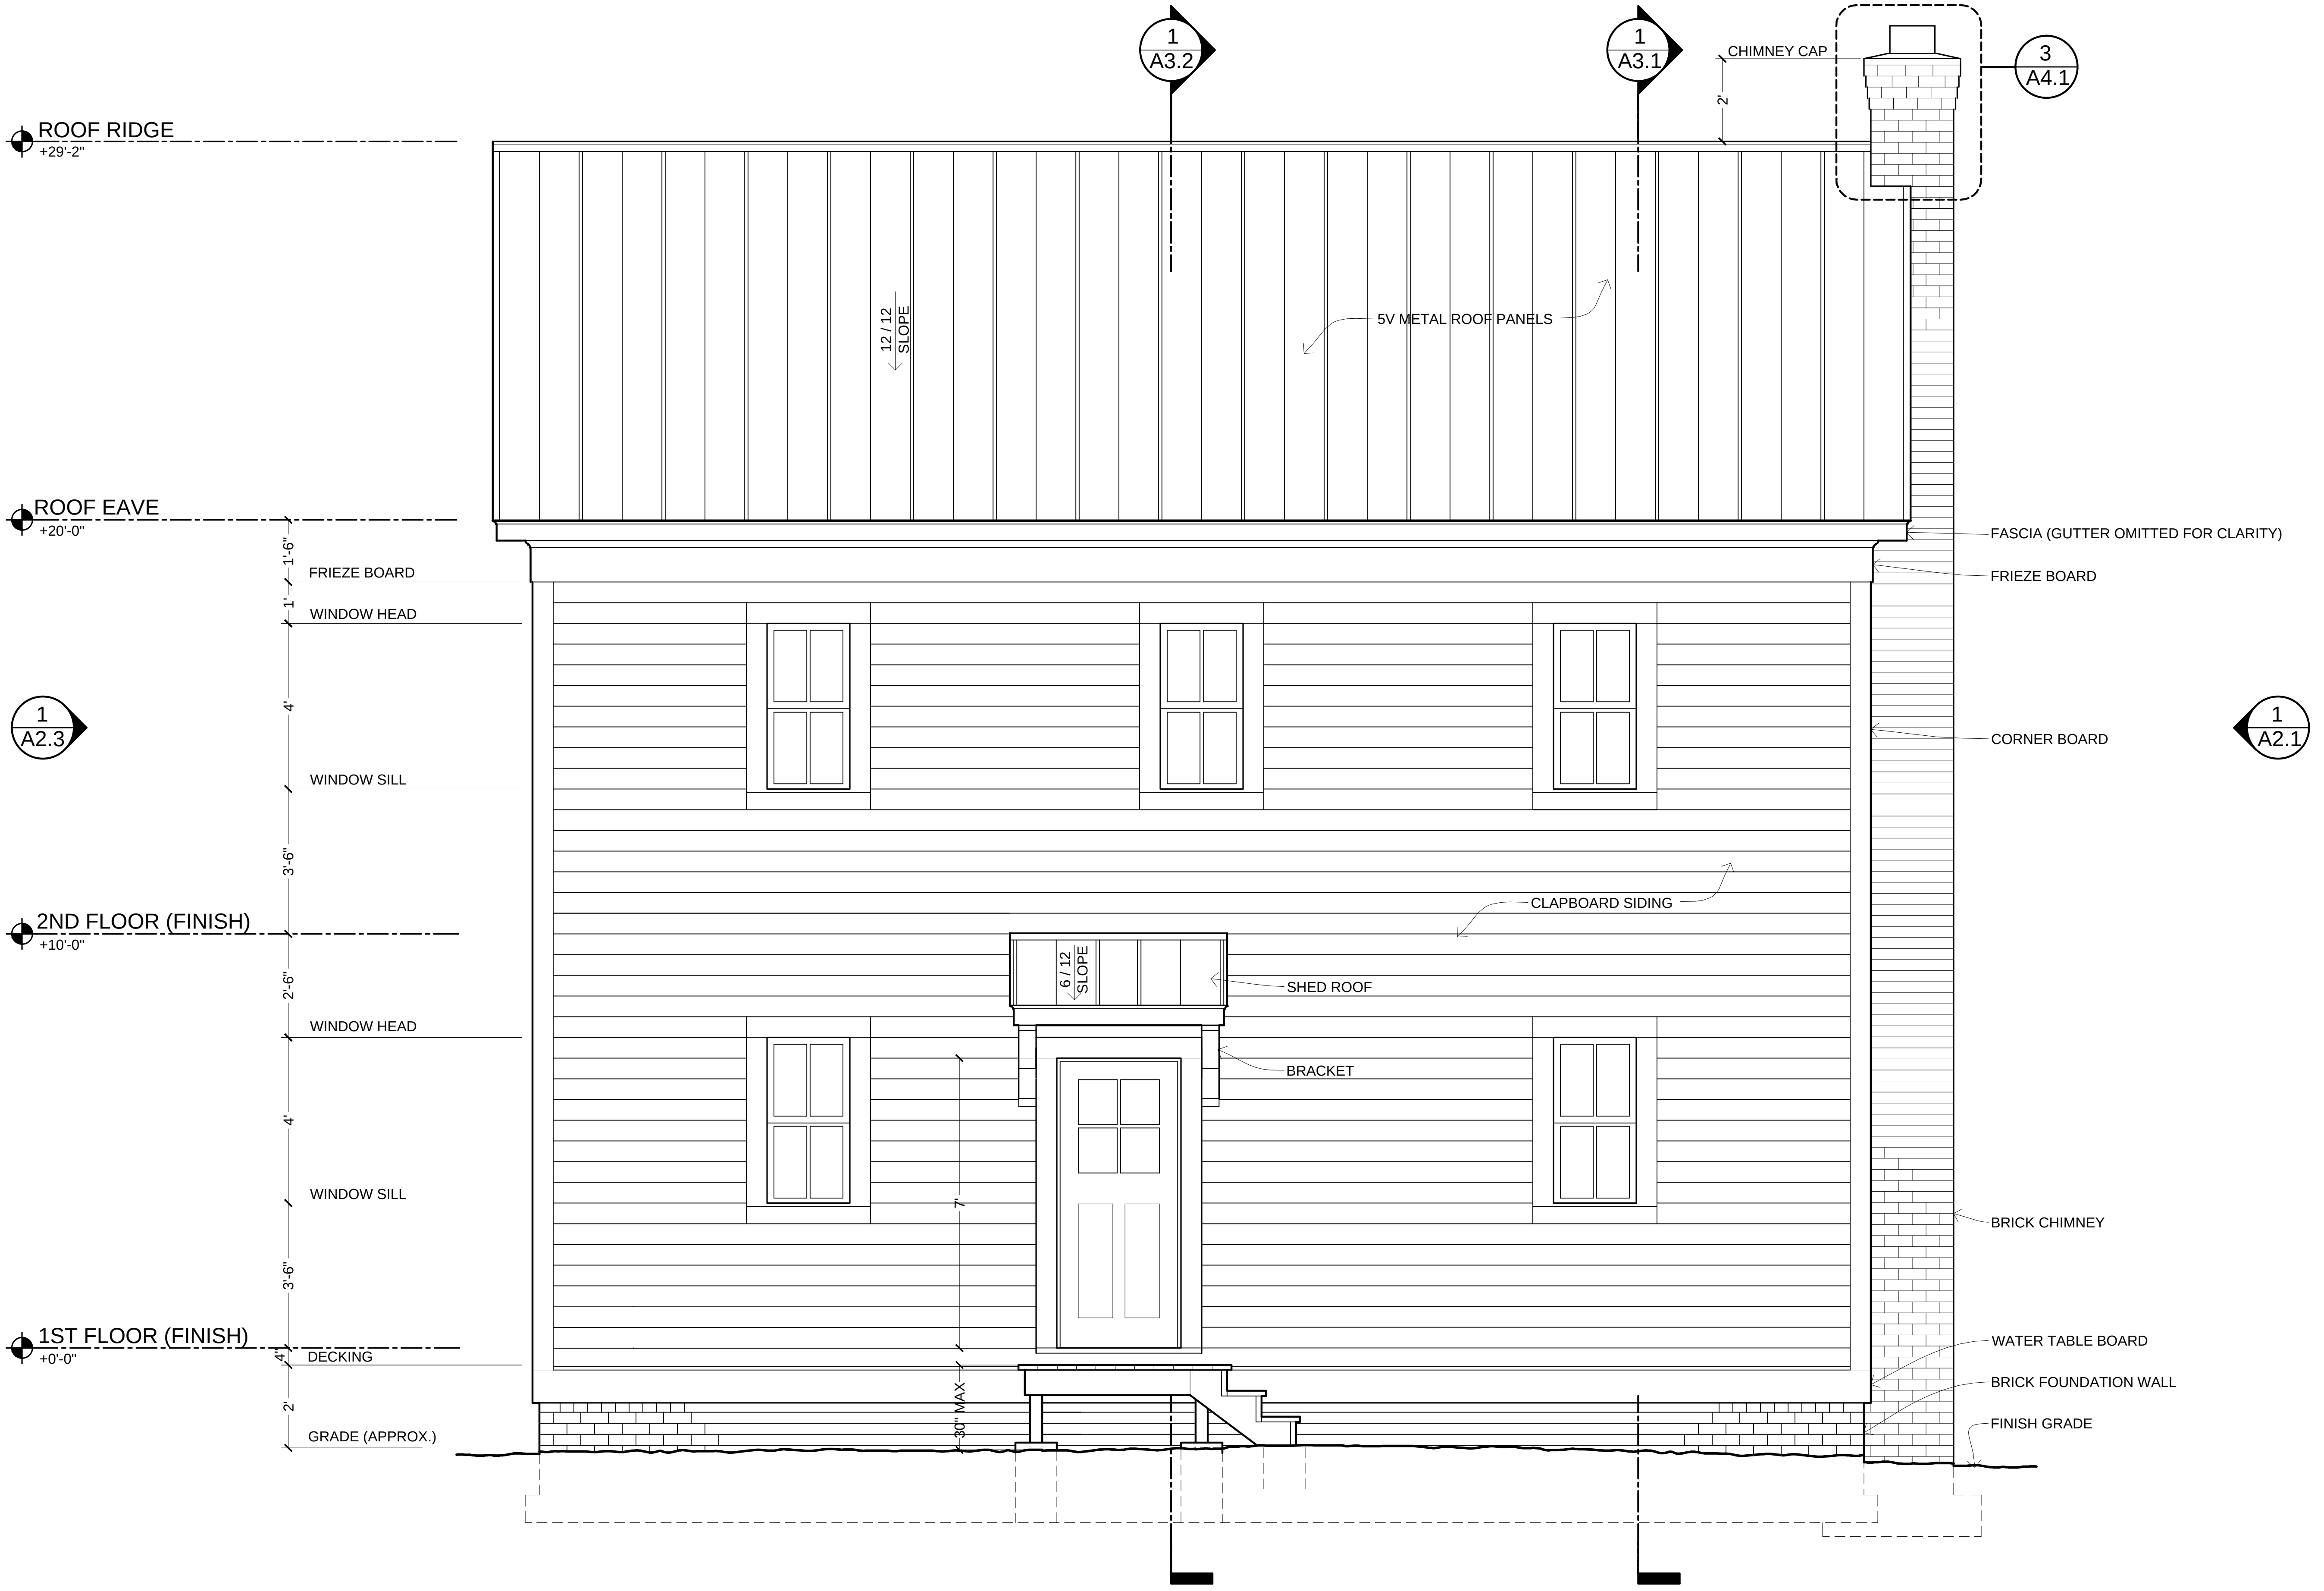

1
A3.2
1
A3.1
CHIMNEY CAP
2'
3
A4.1
ROOF RIDGE
+29'-2"
12 / 12
SLOPE
5V METAL ROOF PANELS
ROOF EAVE
+20'-0"
1'-6"
FRIEZE BOARD
1'
WINDOW HEAD
4'
WINDOW SILL
3'-6"
FASCIA (GUTTER OMITTED FOR CLARITY)
FRIEZE BOARD
1
A2.3
CORNER BOARD
1
A2.1
CLAPBOARD SIDING
2ND FLOOR (FINISH)
+10'-0"
2'-6"
6 / 12
SLOPE
SHED ROOF
WINDOW HEAD
BRACKET
4'
7'
WINDOW SILL
BRICK CHIMNEY
3'-6"
1ST FLOOR (FINISH)
+0'-0"
4"
DECKING
WATER TABLE BOARD
BRICK FOUNDATION WALL
2'
30" MAX
FINISH GRADE
GRADE (APPROX.)

1 BACK ELEVATION (NORTH)

SCALE: 1/4" =1'-0"

THESE DRAWINGS ARE FREE FOR YOU TO SHARE, MODIFY, AND DUPLICATE. THIS WORK DOESN'T REPRESENT A LEGAL CONTRACT OR CONSTITUTE ARCHITECTURAL SERVICES. NO PERSON OR ORGANIZATION MAKES ANY WARRANTY REGARDING THE INFORMATION PROVIDED. THE CREATORS DISCLAIM LIABILITY FOR ANY DAMAGES RESULTING FROM ITS USE. THIS WORK IS AVAILABLE UNDER A CREATIVE COMMONS ATTRIBUTION SHARE-ALIKE LICENSE. SOME RIGHTS RESERVED.

OPEN-SOURCE BLUEPRINTS

CAD FILES AVAILABLE:
www.amatect.com/farmhouse
www.commons.wikimedia.org
/wiki/File:FarmhouseV-001.svg
openarchitecturenetwork.org
/projects/farmhouse

ORIGINAL DESIGNER
Jay Osborne, 2014

VIRGINIA'S FARMHOUSE

123 YELLOW BRICK RD, YOURTOWN, US

REVISION

△	VERSION 0.01 02-15-2015
△	
△	
△	
△	

DATE

02-15-15

SHEET TITLE

NORTH ELEVATION

SHEET NO.

A2.2

THESE DRAWINGS ARE FREE FOR YOU TO SHARE, MODIFY, AND DUPLICATE. THIS WORK DOESN'T REPRESENT A LEGAL CONTRACT OR CONSTITUTE ARCHITECTURAL SERVICES. NO PERSON OR ORGANIZATION MAKES ANY WARRANTY REGARDING THE INFORMATION PROVIDED. THE CREATORS DISCLAIM LIABILITY FOR ANY DAMAGES RESULTING FROM ITS USE. THIS WORK IS AVAILABLE UNDER A CREATIVE COMMONS ATTRIBUTION SHARE-ALIKE LICENSE. SOME RIGHTS RESERVED.

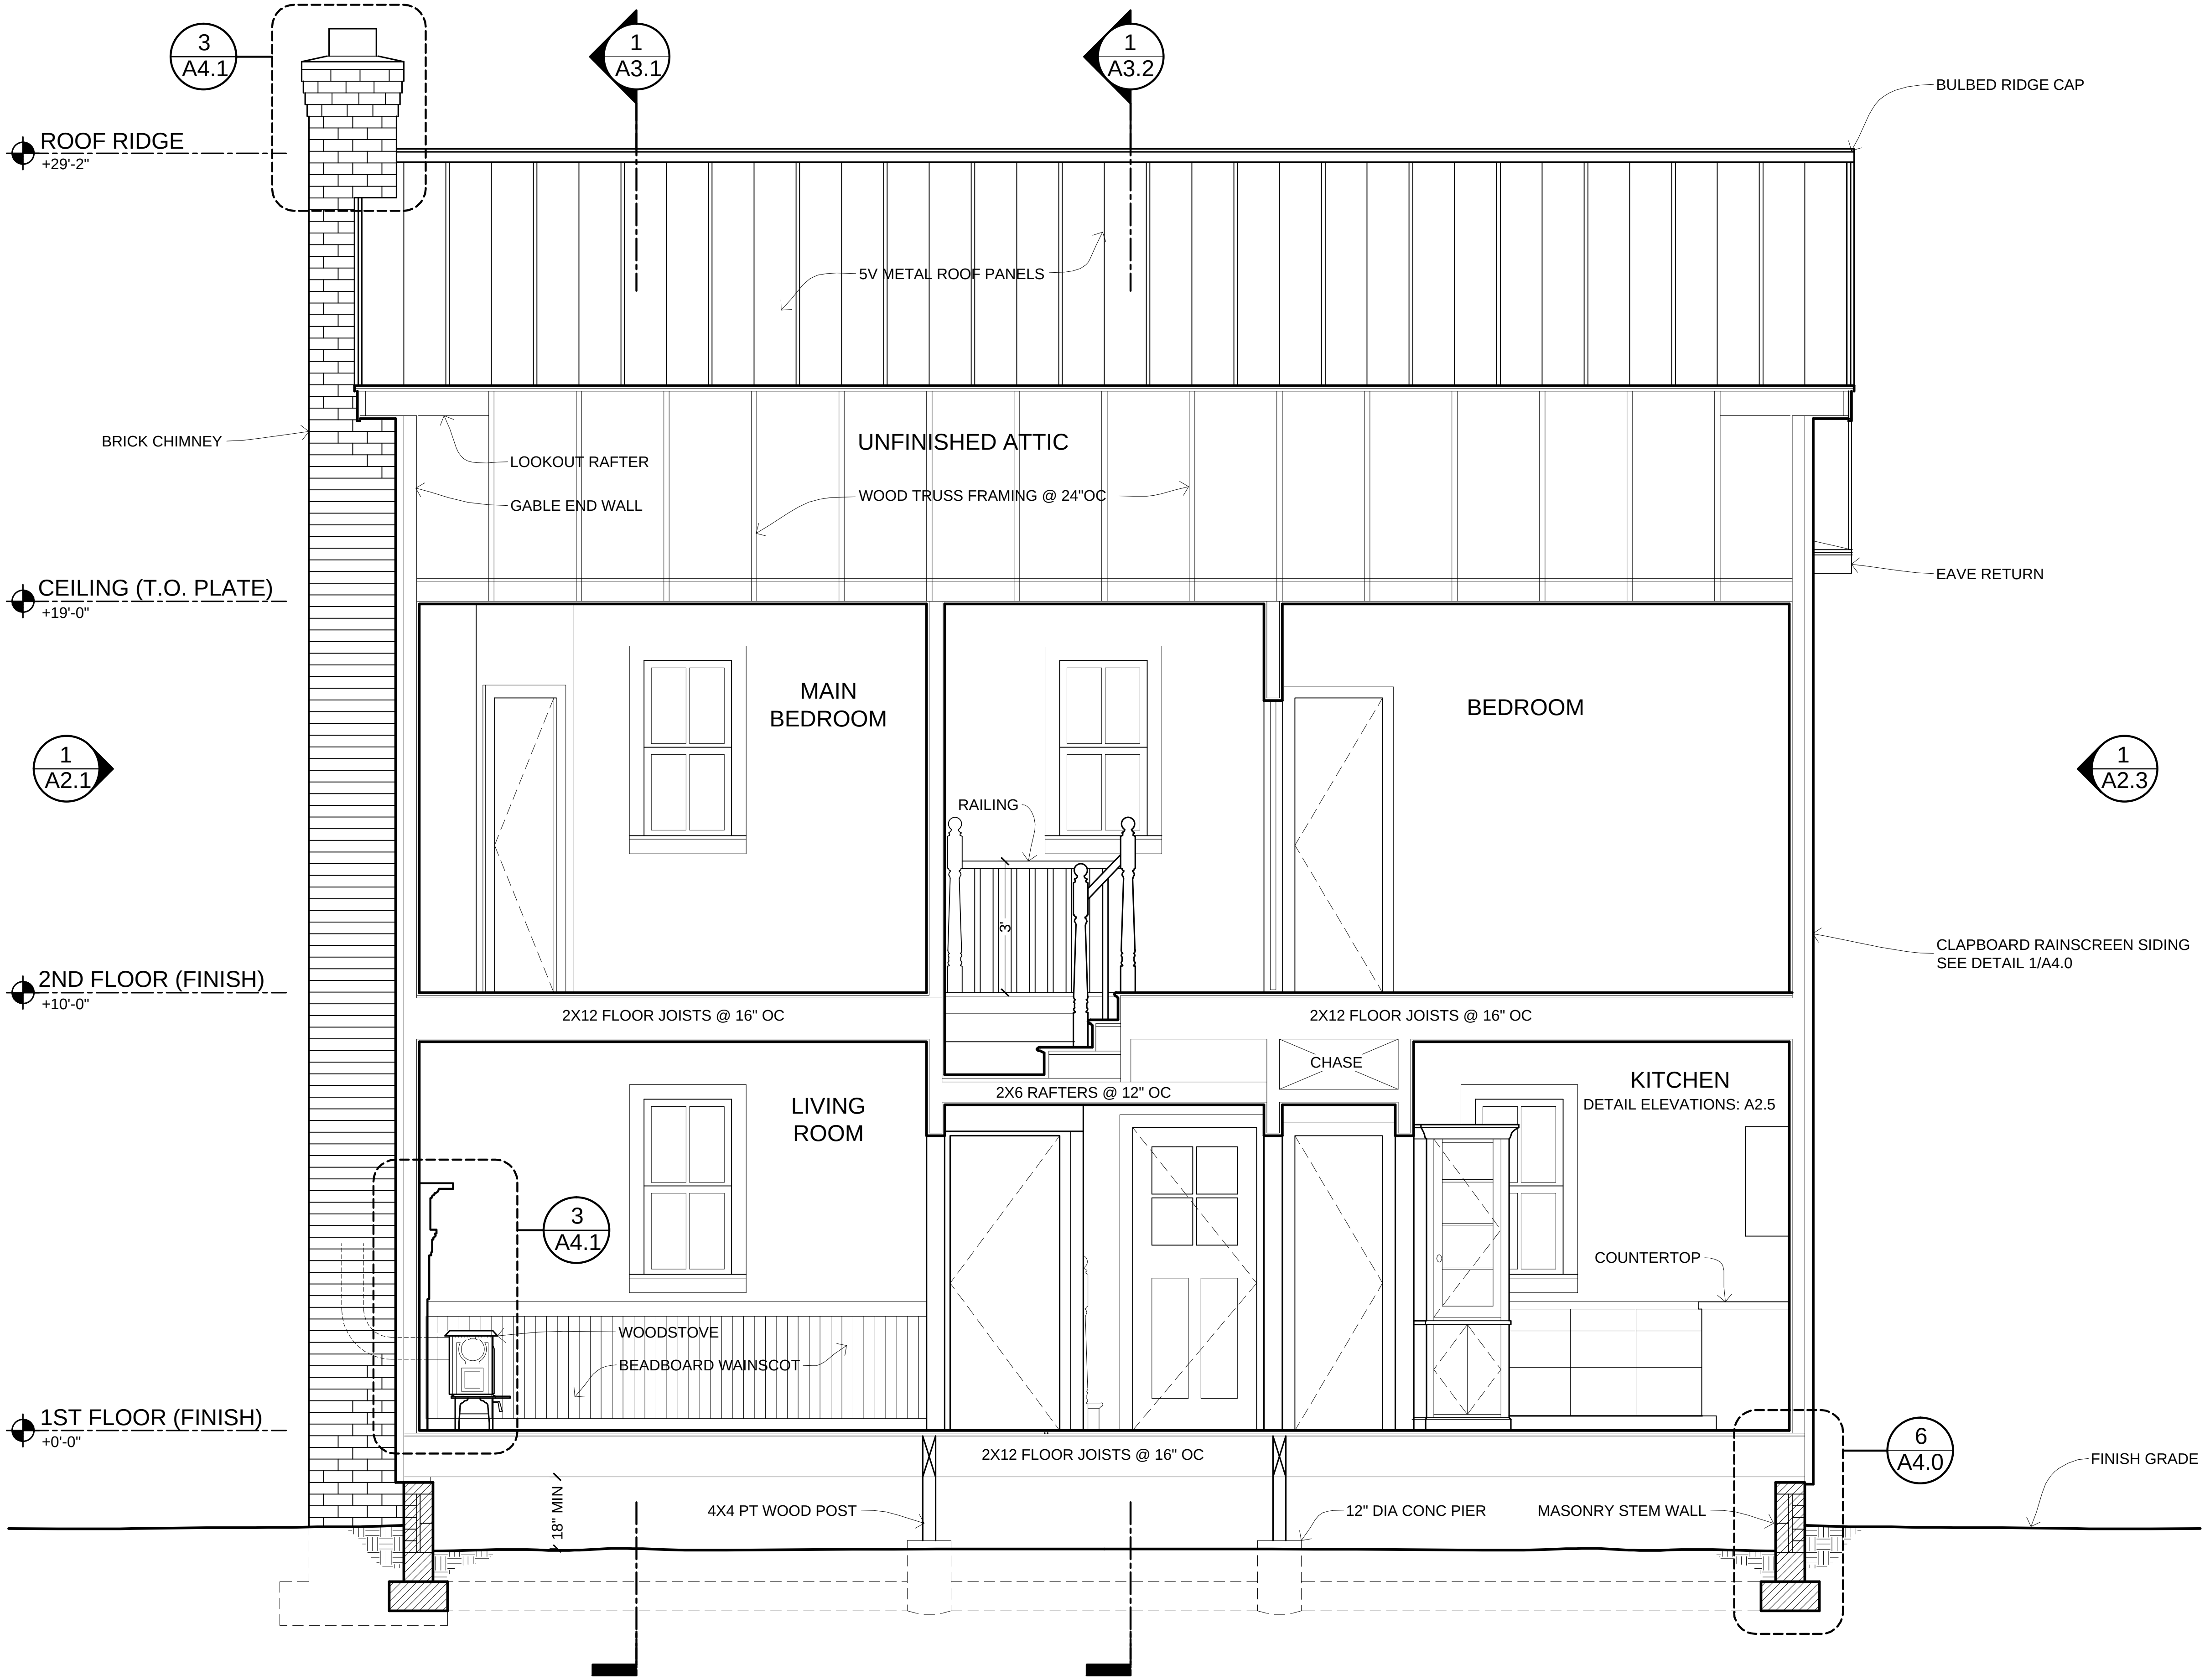
3
A4.1
1
A3.1
1
A3.2
ROOF RIDGE
+29'-2"
BULBED RIDGE CAP
5V METAL ROOF PANELS
BRICK CHIMNEY
UNFINISHED ATTIC
LOOKOUT RAFTER
GABLE END WALL
WOOD TRUSS FRAMING @ 24"OC
EAVE RETURN
CEILING (T.O. PLATE)
+19'-0"
MAIN BEDROOM
BEDROOM
1
A2.1
1
A2.3
RAILING
3'
CLAPBOARD RAINSCREEN SIDING
SEE DETAIL 1/A4.0
2ND FLOOR (FINISH)
+10'-0"
2X12 FLOOR JOISTS @ 16" OC
2X12 FLOOR JOISTS @ 16" OC
CHASE
2X6 RAFTERS @ 12" OC
LIVING ROOM
KITCHEN
DETAIL ELEVATIONS: A2.5
3
A4.1
COUNTERTOP
WOODSTOVE
BEADBOARD WAINSCOT
1ST FLOOR (FINISH)
+0'-0"
2X12 FLOOR JOISTS @ 16" OC
6
A4.0
FINISH GRADE
18" MIN
4X4 PT WOOD POST
12" DIA CONC PIER
MASONRY STEM WALL

① SECTION LOOKING NORTH

SCALE: 1/4" =1'-0"

OPEN-SOURCE BLUEPRINTS

CAD FILES AVAILABLE:
www.amatect.com/farmhouse
www.commons.wikimedia.org
/wiki/File:FarmhouseV-001.svg
openarchitecturenetwork.org
/projects/farmhouse

ORIGINAL DESIGNER
Jay Osborne, 2014

VIRGINIA'S FARMHOUSE

123 YELLOW BRICK RD, YOURTOWN, US

REVISION

△	VERSION 0.01 02-15-2015
△	
△	
△	
△	

DATE

02-15-15

SHEET TITLE

BUILDING SECTION

SHEET NO.

A3.0

THESE DRAWINGS ARE FREE FOR YOU TO SHARE, MODIFY, AND DUPLICATE. THIS WORK DOESN'T REPRESENT A LEGAL CONTRACT OR CONSTITUTE ARCHITECTURAL SERVICES. NO PERSON OR ORGANIZATION MAKES ANY WARRANTY REGARDING THE INFORMATION PROVIDED. THE CREATORS DISCLAIM LIABILITY FOR ANY DAMAGES RESULTING FROM ITS USE. THIS WORK IS AVAILABLE UNDER A CREATIVE COMMONS ATTRIBUTION SHARE-ALIKE LICENSE. SOME RIGHTS RESERVED.

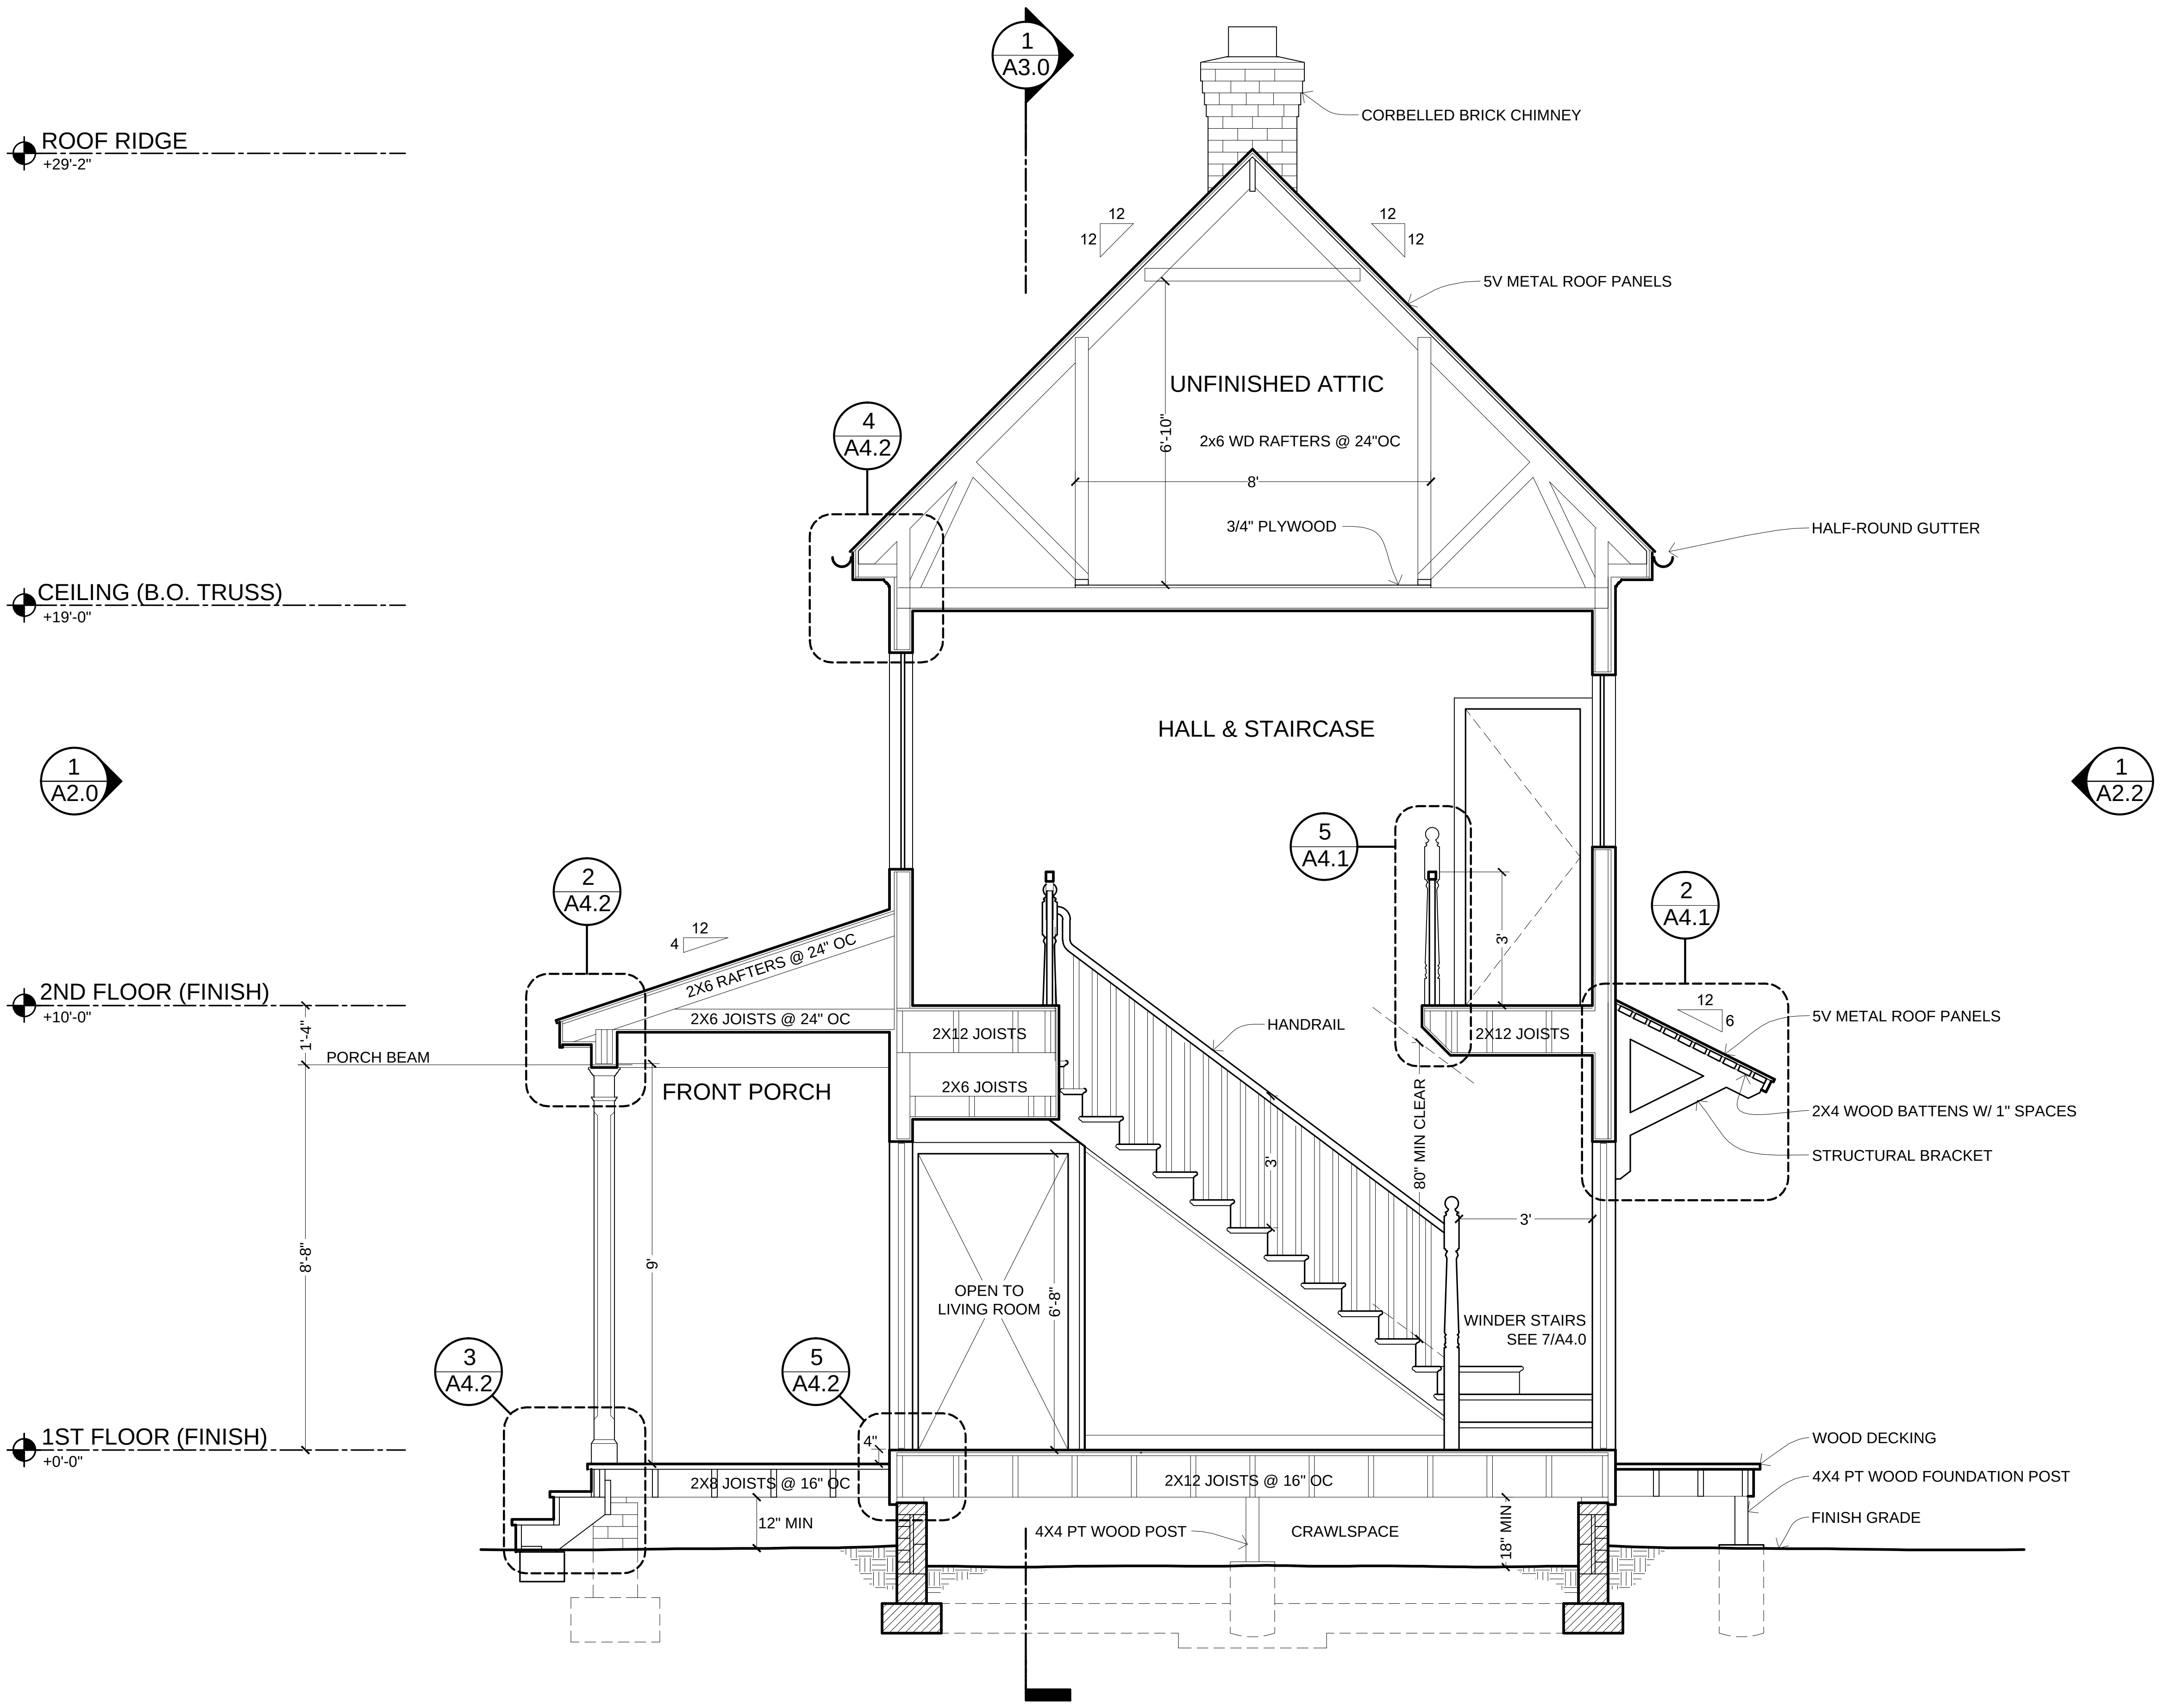
1
A3.0
ROOF RIDGE
+29'-2"
CORBELLED BRICK CHIMNEY
12
12
12
12
5V METAL ROOF PANELS
UNFINISHED ATTIC
6'-10"
2x6 WD RAFTERS @ 24"OC
4
A4.2
8'
3/4" PLYWOOD
HALF-ROUND GUTTER
CEILING (B.O. TRUSS)
+19'-0"
HALL & STAIRCASE
1
A2.0
1
A2.2
5
A4.1
2
A4.2
2
A4.1
4
12
2X6 RAFTERS @ 24" OC
3'
2ND FLOOR (FINISH)
+10'-0"
2X6 JOISTS @ 24" OC
2X12 JOISTS
HANDRAIL
2X12 JOISTS
12
6
5V METAL ROOF PANELS
1'-4"
PORCH BEAM
FRONT PORCH
2X6 JOISTS
80" MIN CLEAR
2X4 WOOD BATTENS W/ 1" SPACES
STRUCTURAL BRACKET
3'
3'
8'-8"
9'
OPEN TO
LIVING ROOM
6'-8"
WINDER STAIRS
SEE 7/A4.0
3
A4.2
5
A4.2
4"
1ST FLOOR (FINISH)
+0'-0"
WOOD DECKING
2X8 JOISTS @ 16" OC
2X12 JOISTS @ 16" OC
4X4 PT WOOD FOUNDATION POST
12" MIN
4X4 PT WOOD POST
CRAWLSPACE
18" MIN
FINISH GRADE

1 SECTION THROUGH CENTRAL HALL AND STAIRCASE

SCALE: 1/4" =1'-0"

OPEN-SOURCE BLUEPRINTS

CAD FILES AVAILABLE:
www.amatect.com/farmhouse
www.commons.wikimedia.org
/wiki/File:FarmhouseV-001.svg
openarchitecturenetwork.org
/projects/farmhouse

ORIGINAL DESIGNER
Jay Osborne, 2014

VIRGINIA'S FARMHOUSE

123 YELLOW BRICK RD, YOURTOWN, US

REVISION

△	VERSION 0.01 02-15-2015
△	
△	
△	
△	

DATE

02-15-15

SHEET TITLE

SECTIONS

SHEET NO.

A3.2