THESE DRAWINGS ARE FREE FOR YOU TO SHARE, MODIFY, AND DUPLICATE. THIS WORK DOESN'T REPRESENT A LEGAL CONTRACT OR CONSTITUTE ARCHITECTURAL SERVICES. NO PERSON OR ORGANIZATION MAKES ANY WARRANTY REGARDING THE INFORMATION PROVIDED. THE CREATORS DISCLAIM LIABILITY FOR ANY DAMAGES RESULTING FROM ITS USE. THIS WORK IS AVAILABLE UNDER A CREATIVE COMMONS ATTRIBUTION SHARE-ALIKE LICENSE. SOME RIGHTS RESERVED.

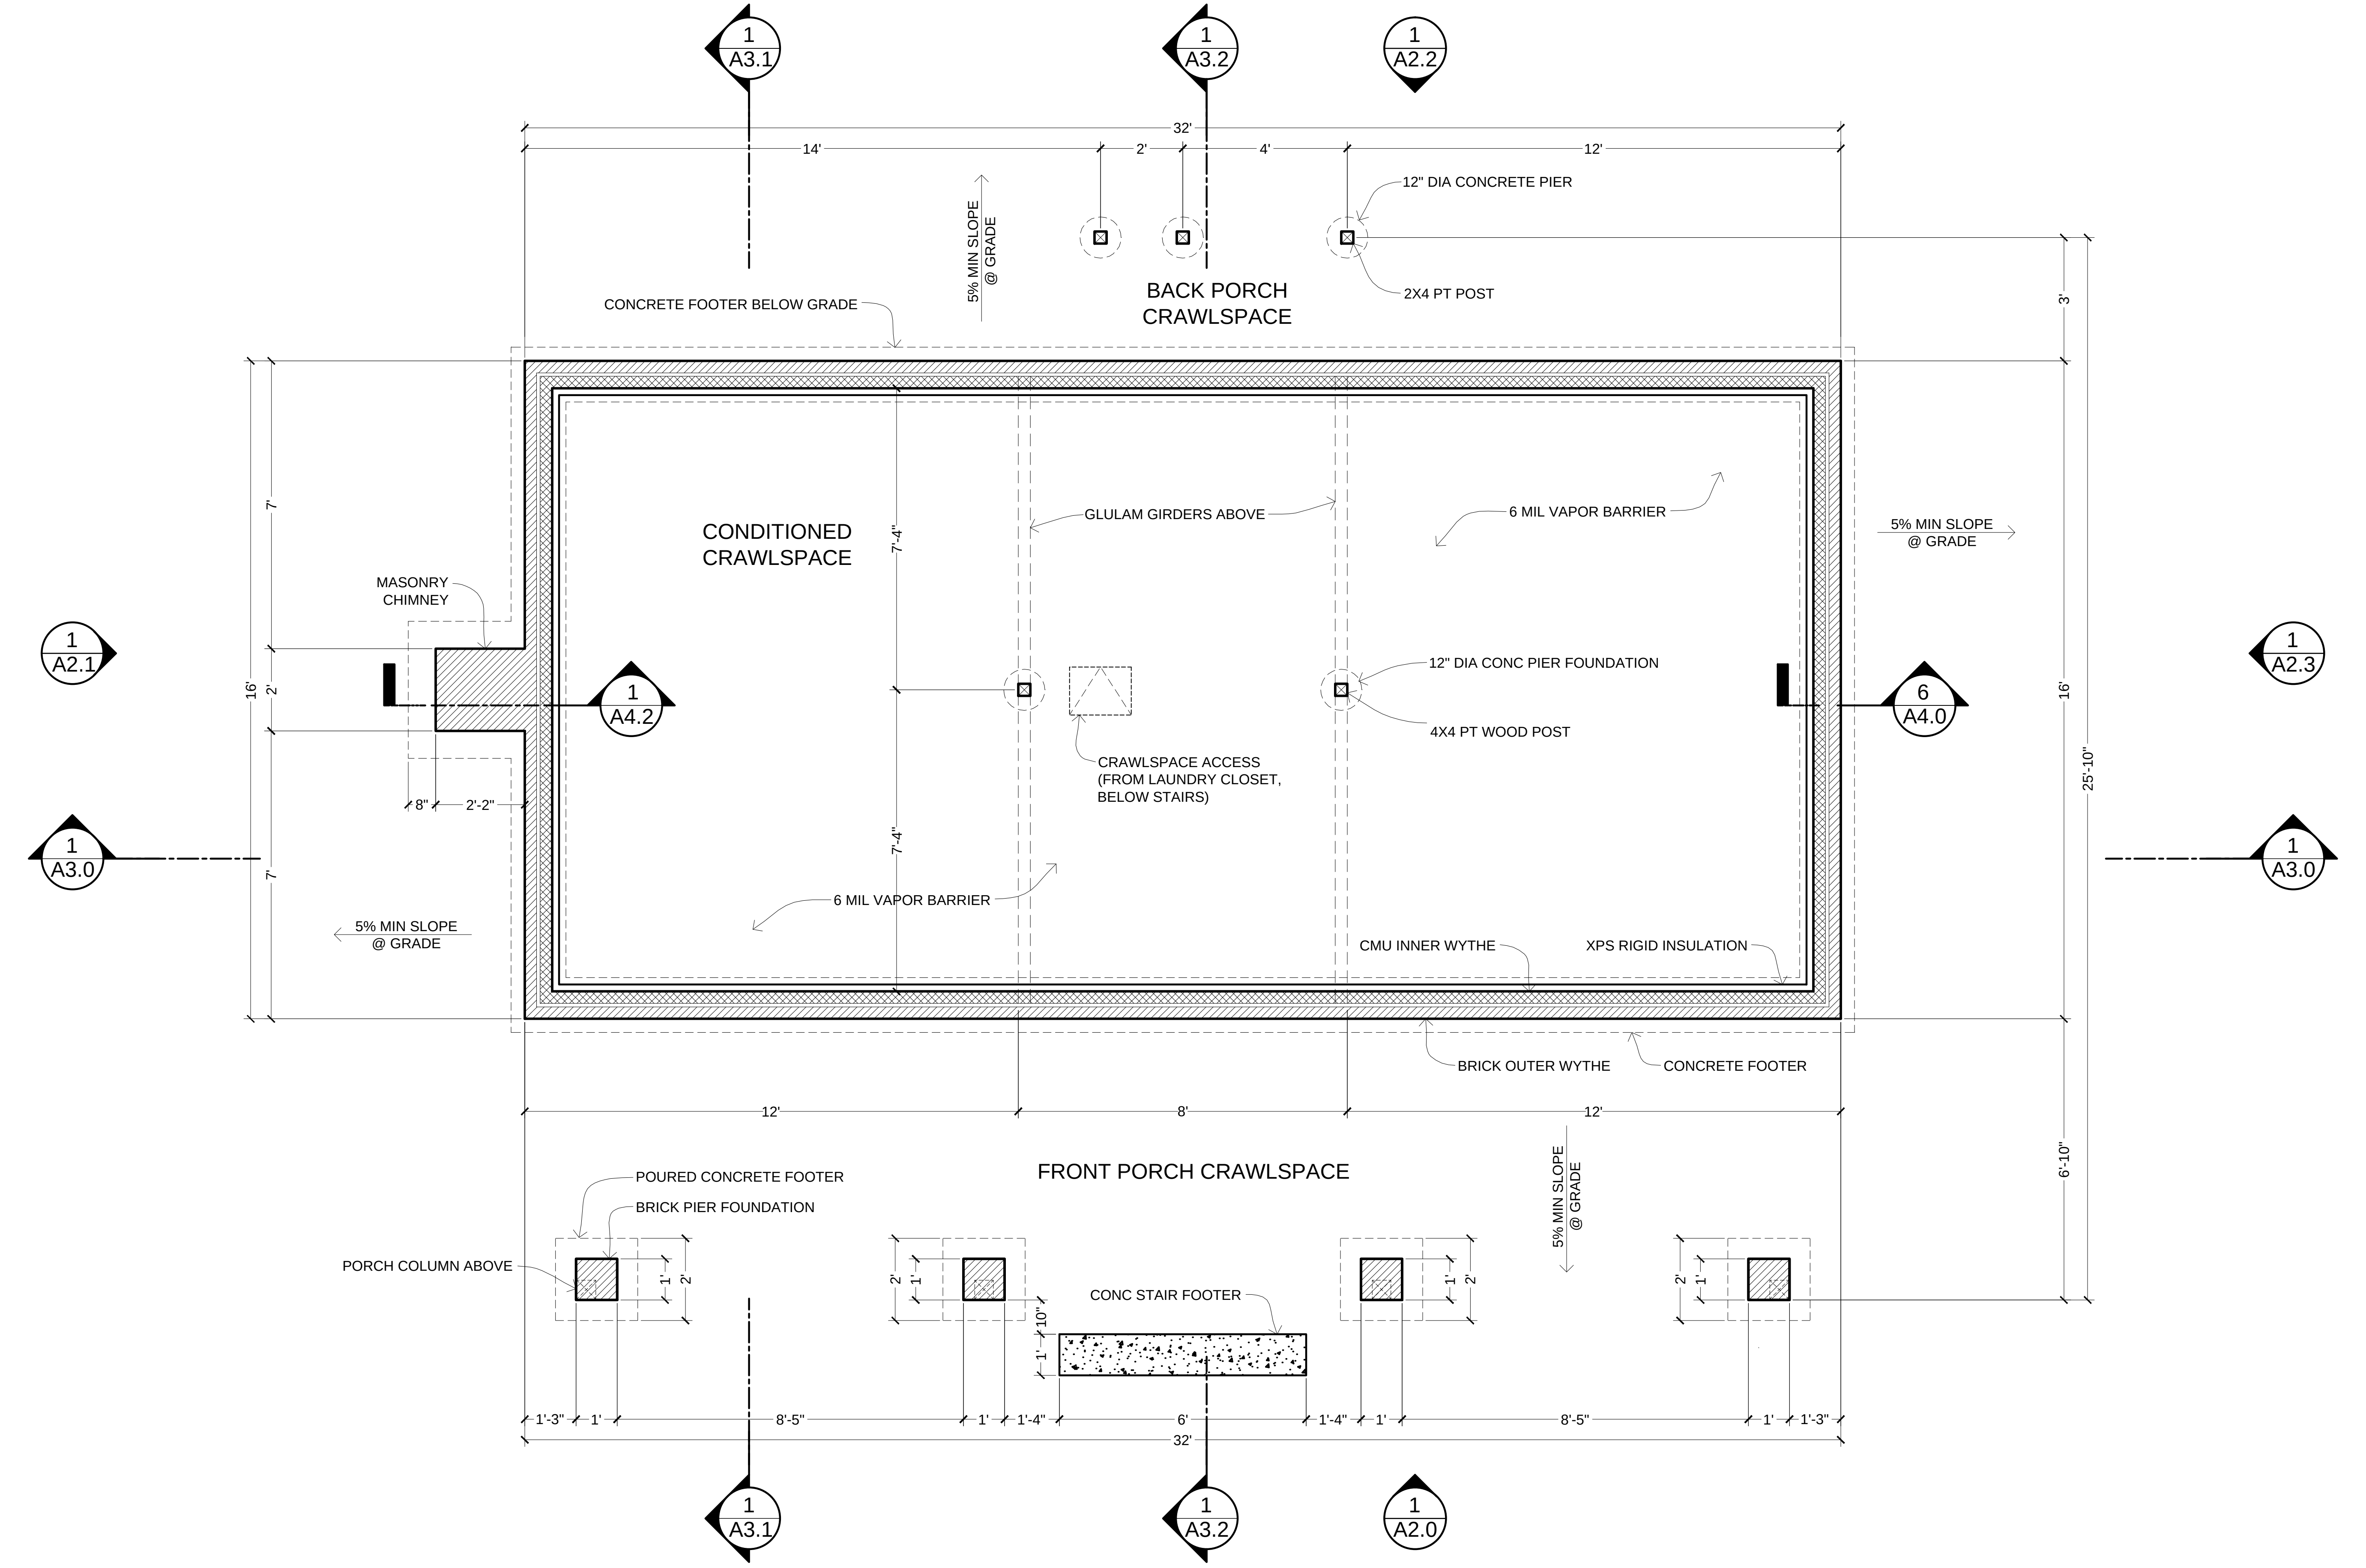

① FOUNDATION PLAN

SCALE: 1/4" =1'-0"

N

OPEN-SOURCE BLUEPRINTS

CAD FILES AVAILABLE:
www.amatect.com/farmhouse
www.commons.wikimedia.org
/wiki/File:FarmhouseV-001.svg
openarchitecturenetwork.org
/projects/farmhouse

ORIGINAL DESIGNER
Jay Osborne, 2014

VIRGINIA'S FARMHOUSE

123 YELLOW BRICK RD, YOURTOWN, US

REVISION

△	VERSION 0.01 02-15-2015
△	
△	
△	
△	

DATE

02-15-15

SHEET TITLE

FOUNDATION PLAN

SHEET NO.

A1.1

THESE DRAWINGS ARE FREE FOR YOU TO SHARE, MODIFY, AND DUPLICATE. THIS WORK DOESN'T REPRESENT A LEGAL CONTRACT OR CONSTITUTE ARCHITECTURAL SERVICES. NO PERSON OR ORGANIZATION MAKES ANY WARRANTY REGARDING THE INFORMATION PROVIDED. THE CREATORS DISCLAIM LIABILITY FOR ANY DAMAGES RESULTING FROM ITS USE. THIS WORK IS AVAILABLE UNDER A CREATIVE COMMONS ATTRIBUTION SHARE-ALIKE LICENSE. SOME RIGHTS RESERVED.

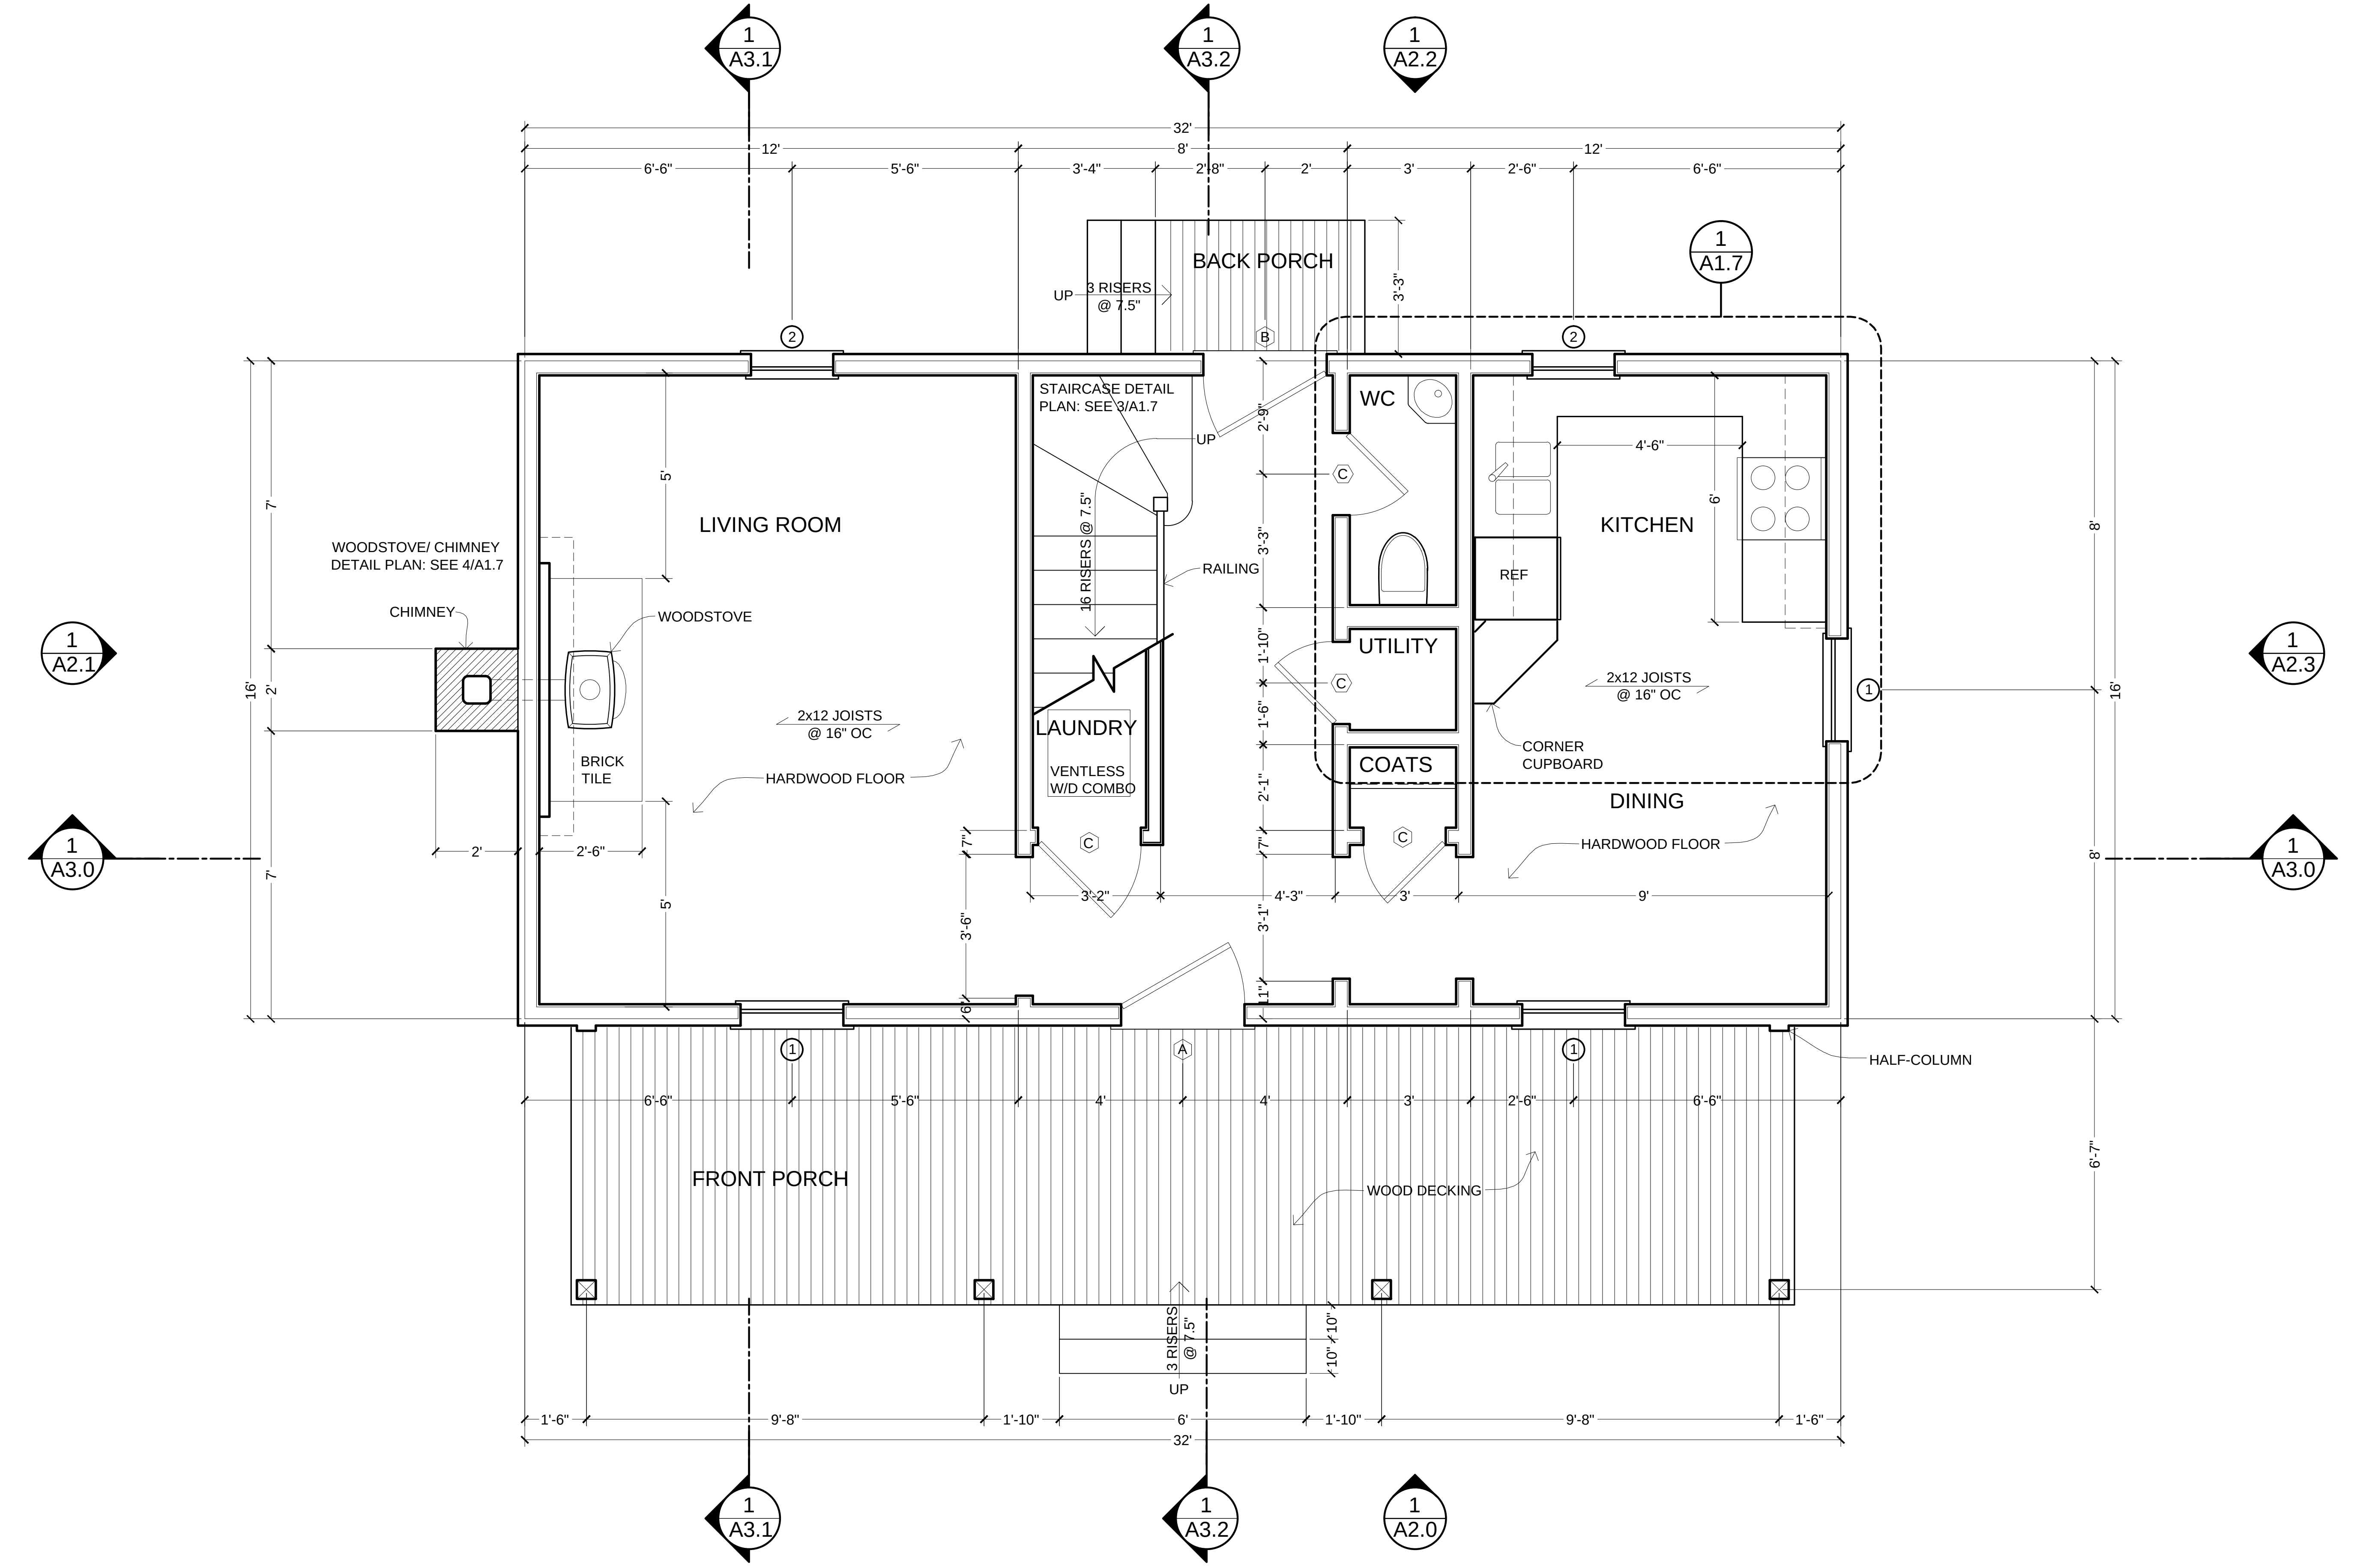

① 1ST FLOOR PLAN

SCALE: 1/4" =1'-0"

N

OPEN-SOURCE BLUEPRINTS

CAD FILES AVAILABLE:
www.amatect.com/farmhouse
www.commons.wikimedia.org /wiki/File:FarmhouseV-001.svg
openarchitecturenetwork.org /projects/farmhouse

ORIGINAL DESIGNER
Jay Osborne, 2014

VIRGINIA'S FARMHOUSE

123 YELLOW BRICK RD, YOURTOWN, US

REVISION

△	VERSION 0.01 02-15-2015
△	
△	
△	
△	

DATE
02-15-15

SHEET TITLE
1ST FLOOR PLAN

SHEET NO.
A1.2

THESE DRAWINGS ARE FREE FOR YOU TO SHARE, MODIFY, AND DUPLICATE. THIS WORK DOESN'T REPRESENT A LEGAL CONTRACT OR CONSTITUTE ARCHITECTURAL SERVICES. NO PERSON OR ORGANIZATION MAKES ANY WARRANTY REGARDING THE INFORMATION PROVIDED. THE CREATORS DISCLAIM LIABILITY FOR ANY DAMAGES RESULTING FROM ITS USE. THIS WORK IS AVAILABLE UNDER A CREATIVE COMMONS ATTRIBUTION SHARE-ALIKE LICENSE. SOME RIGHTS RESERVED.

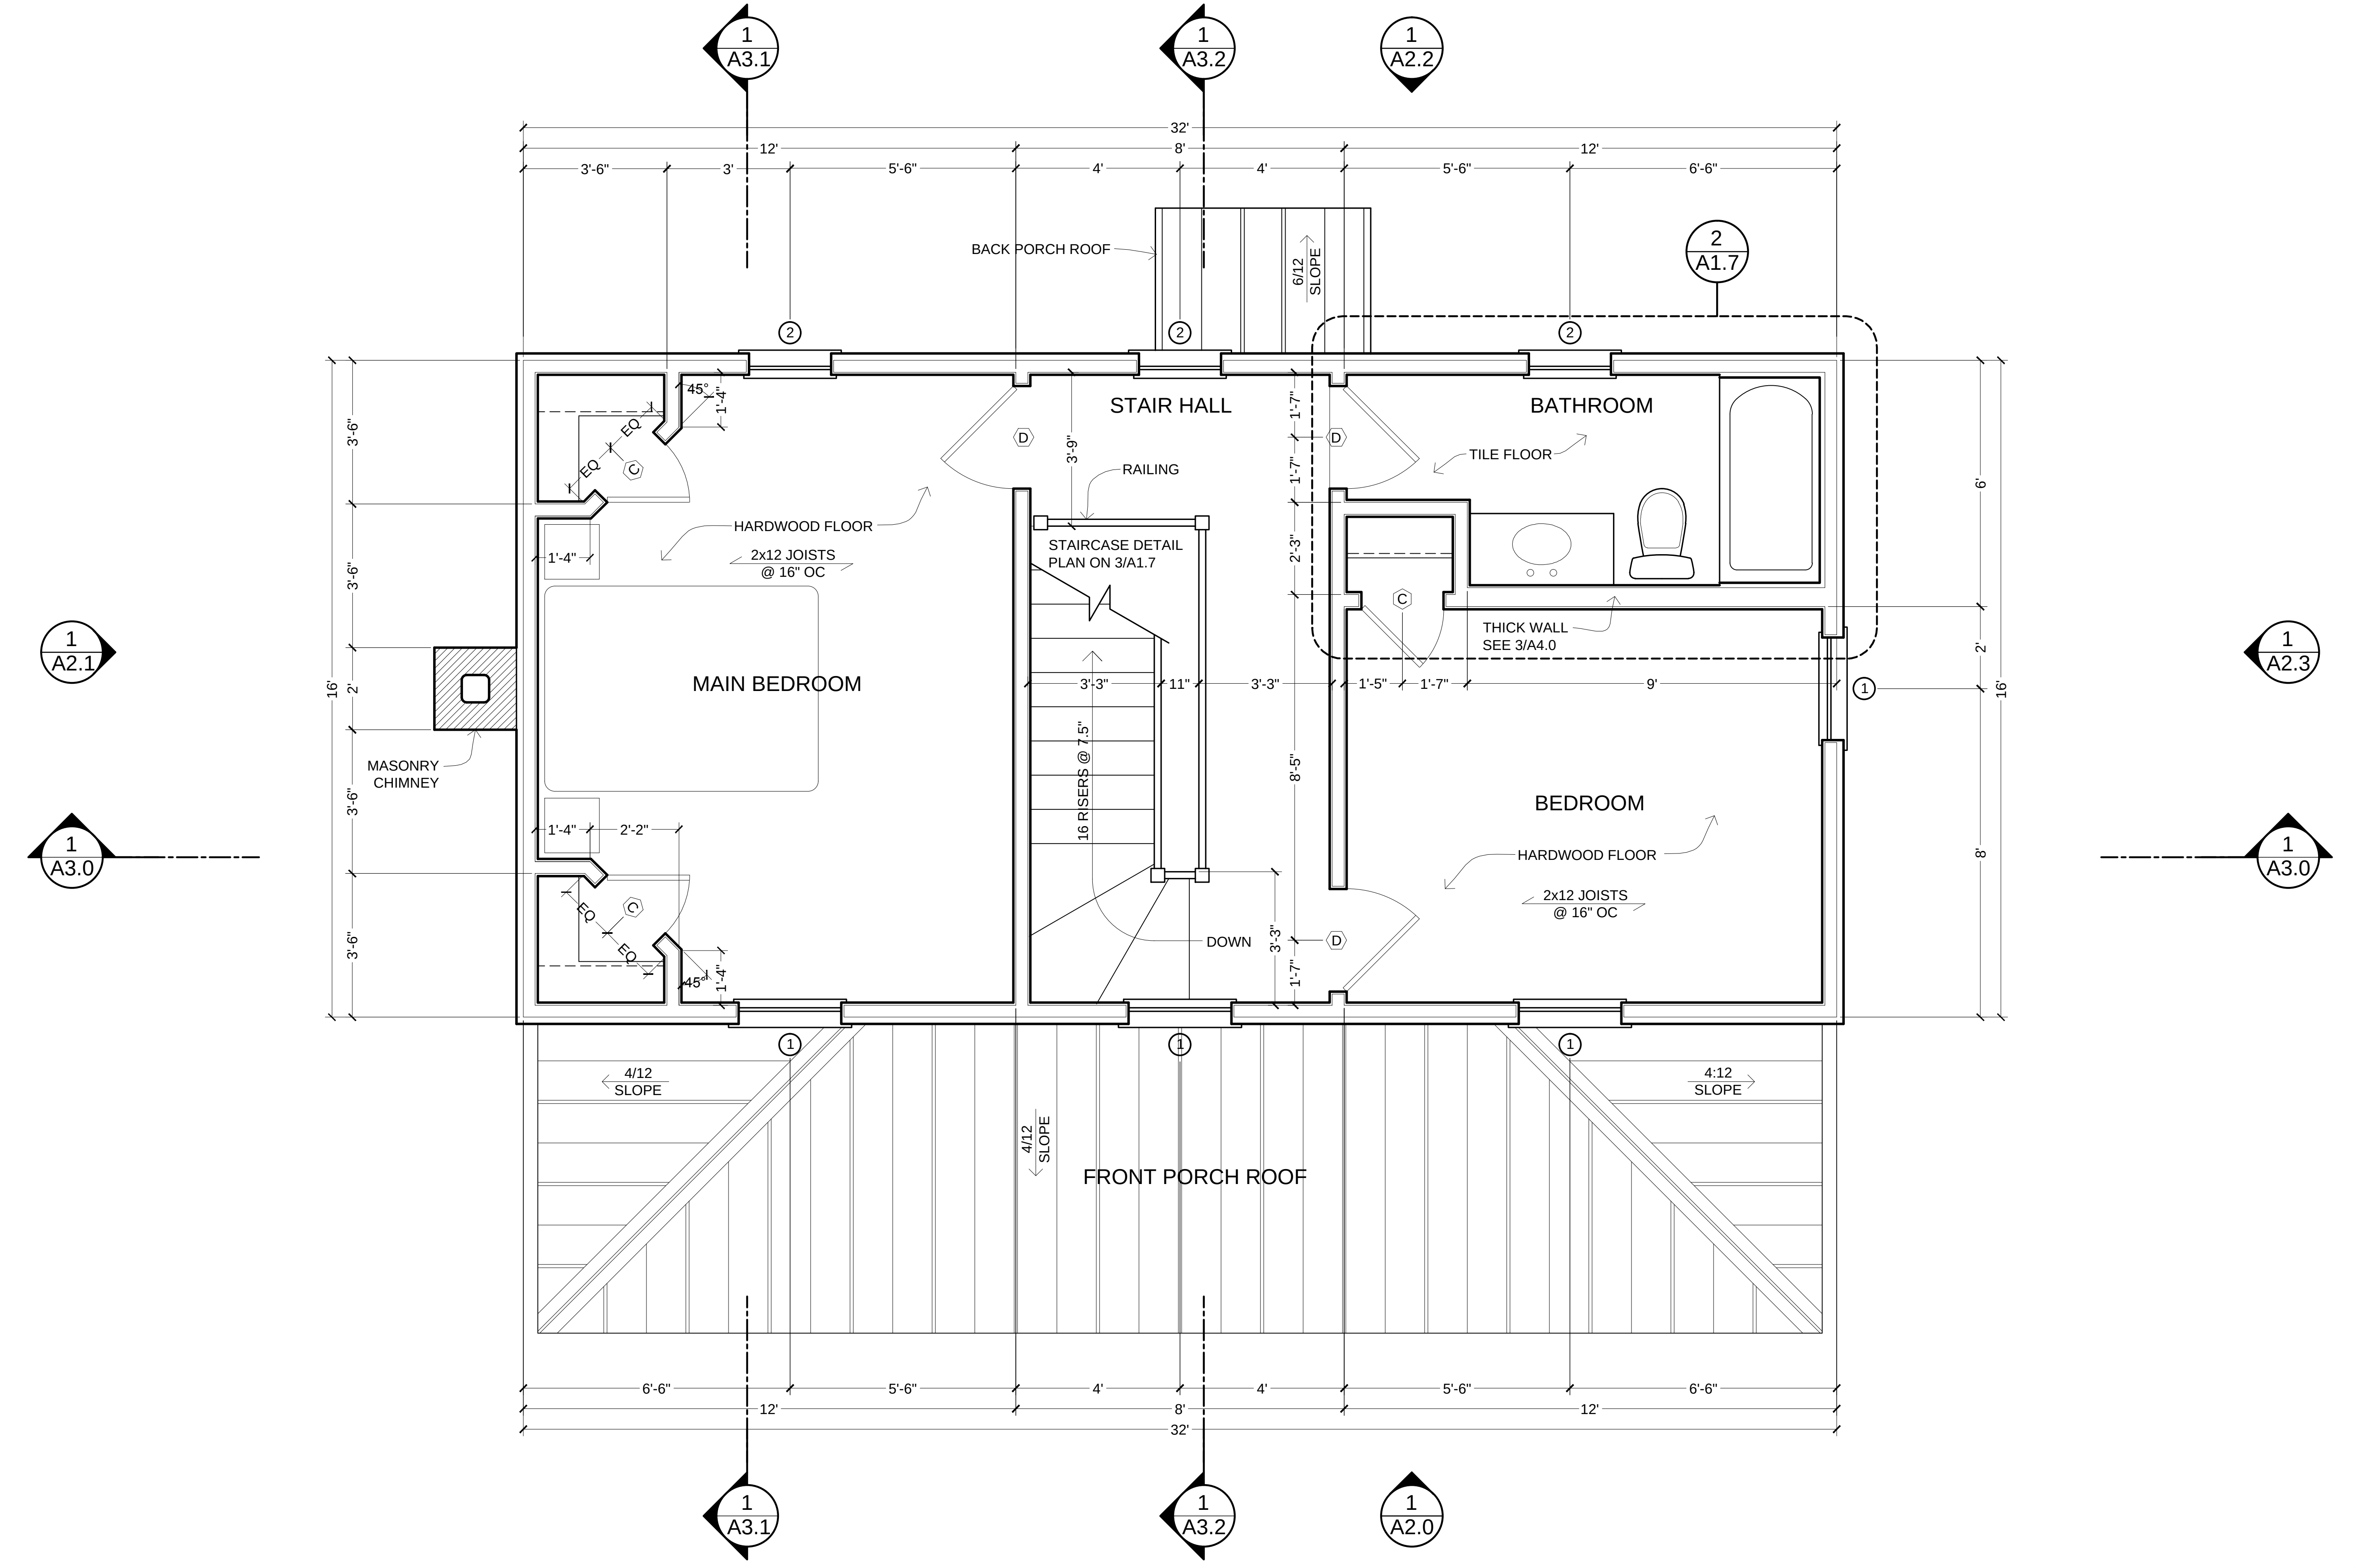

2ND FLOOR PLAN

SCALE: 1/4" =1'-0"

OPEN-SOURCE BLUEPRINTS

CAD FILES AVAILABLE:
www.amatect.com/farmhouse
www.commons.wikimedia.org
/wiki/File:FarmhouseV-001.svg
openarchitecturenetwork.org
/projects/farmhouse

ORIGINAL DESIGNER
Jay Osborne, 2014

VIRGINIA'S FARMHOUSE

123 YELLOW BRICK RD, YOURTOWN, US

REVISION

VERSION 0.01
02-15-2015

DATE

02-15-15

SHEET TITLE

2ND FLOOR PLAN

SHEET NO.

A1.3

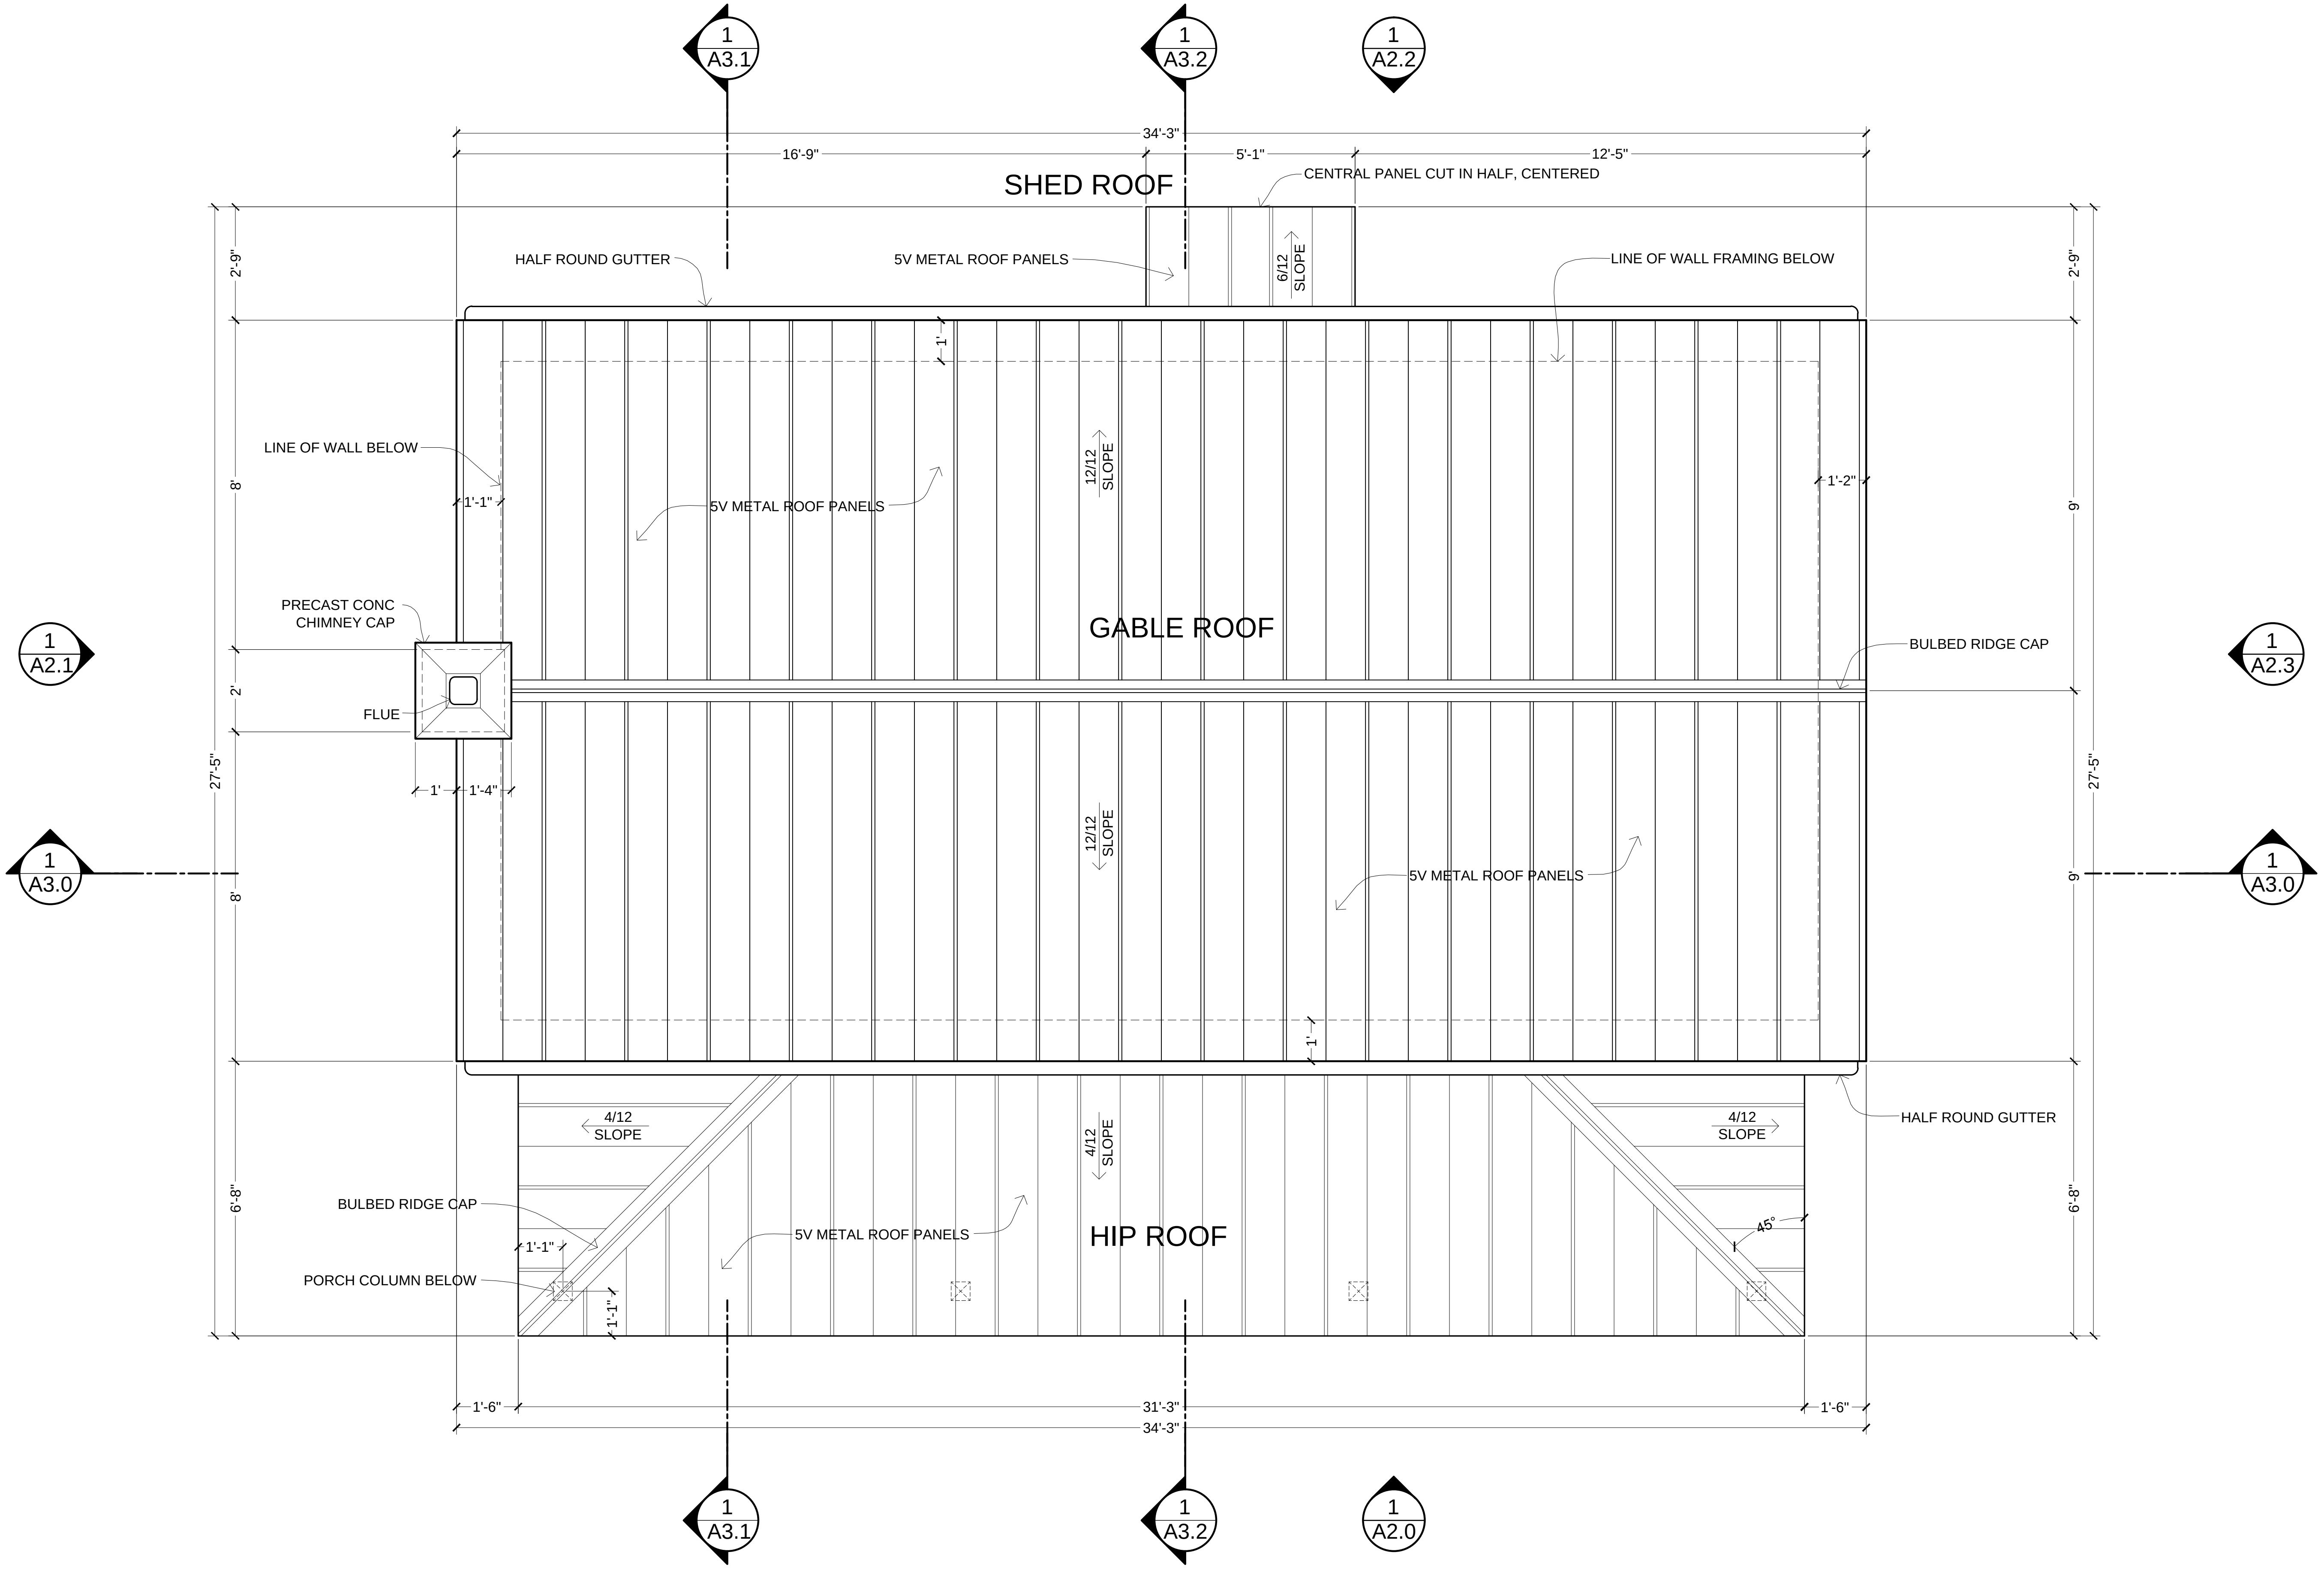

① ROOF PLAN
SCALE: 1/4" =1'-0"

THESE DRAWINGS ARE FREE FOR YOU TO SHARE, MODIFY, AND DUPLICATE. THIS WORK DOESN'T REPRESENT A LEGAL CONTRACT OR CONSTITUTE ARCHITECTURAL SERVICES. NO PERSON OR ORGANIZATION MAKES ANY WARRANTY REGARDING THE INFORMATION PROVIDED. THE CREATORS DISCLAIM LIABILITY FOR ANY DAMAGES RESULTING FROM ITS USE. THIS WORK IS AVAILABLE UNDER A CREATIVE COMMONS ATTRIBUTION SHARE-ALIKE LICENSE. SOME RIGHTS RESERVED.

OPEN-SOURCE BLUEPRINTS

CAD FILES AVAILABLE:
www.amatect.com/farmhouse
www.commons.wikimedia.org/wiki/File:FarmhouseV-001.svg
openarchitecturenetwork.org/projects/farmhouse

ORIGINAL DESIGNER
Jay Osborne, 2014

VIRGINIA'S FARMHOUSE

123 YELLOW BRICK RD, YOURTOWN, US

REVISION
VERSION 0.01
02-15-2015

DATE
02-15-15

SHEET TITLE
ROOF PLAN

SHEET NO.
A1.4